

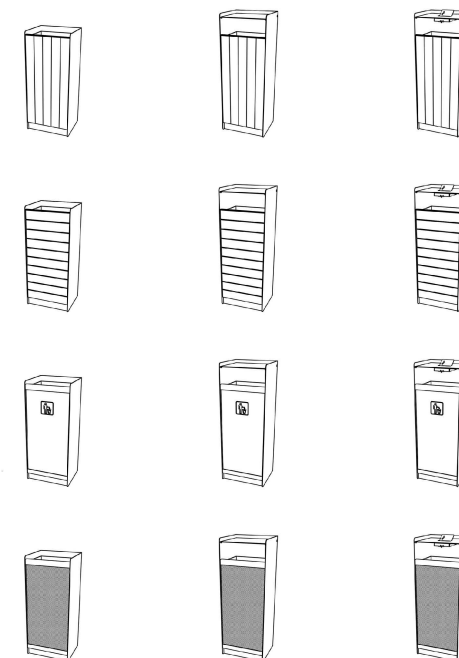
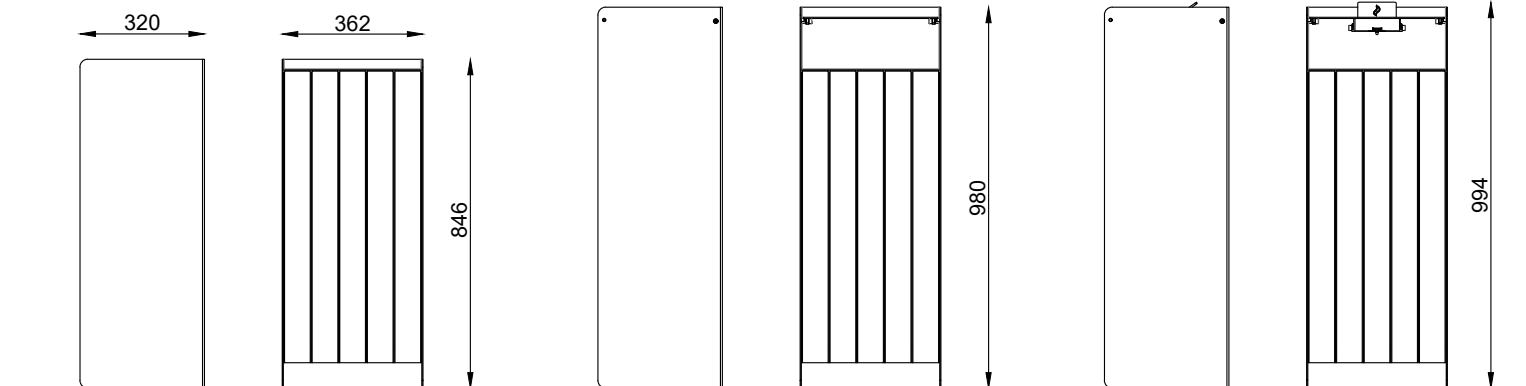


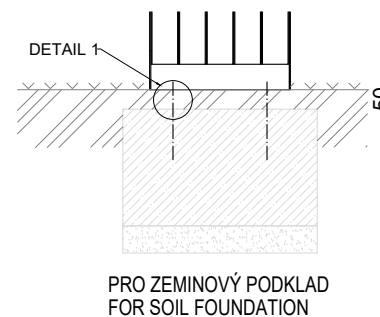

0.08 m³
beton C 12/15
concrete C 12/15


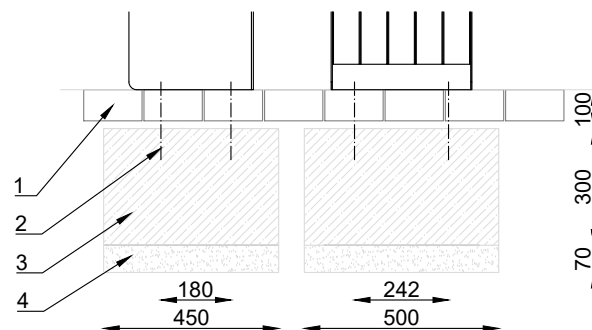


LEGENDA:

- 1 Dlažba
- 2 Chemická kotva M10, dl. min 200 mm
- 3 Betonový základ
- 4 Štěrkové lože ztuhlé, tl. min. 70 mm
- 5 Kontramatice (pro zeminový podklad)

LEGEND:

- 1 Pavement
- 2 Chemical anchor M10, dl. min 200 mm
- 3 Concrete foundation
- 4 Compacted gravel base, depth min. 70 mm
- 5 Counter nuts (for soil foundation)

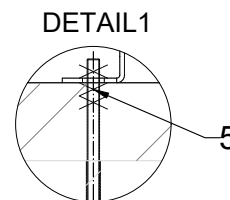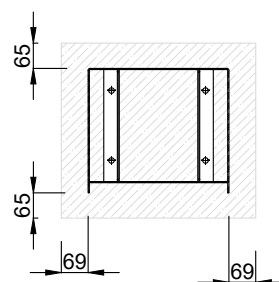

KMA211 KMA231
KMA212 KMA232
KMA213 KMA233
KMA221 KMA241
KMA222 KMA242
KMA223 KMA243

Všechna práva vyhrazena. Chráněno průmyslovým vzorem.
All rights reserved. Protection of industrial design.

Rozměry výrobků, základů a kotvení jsou pouze orientační. Přesné rozměry obdržíte při zpracování nabídky naším obchodním oddělením.
Dimensions of products, foundations and anchors are informative only. The exact dimensions you get with our offer.

STREETPARK

version: 2021/05
streetpark.eu