

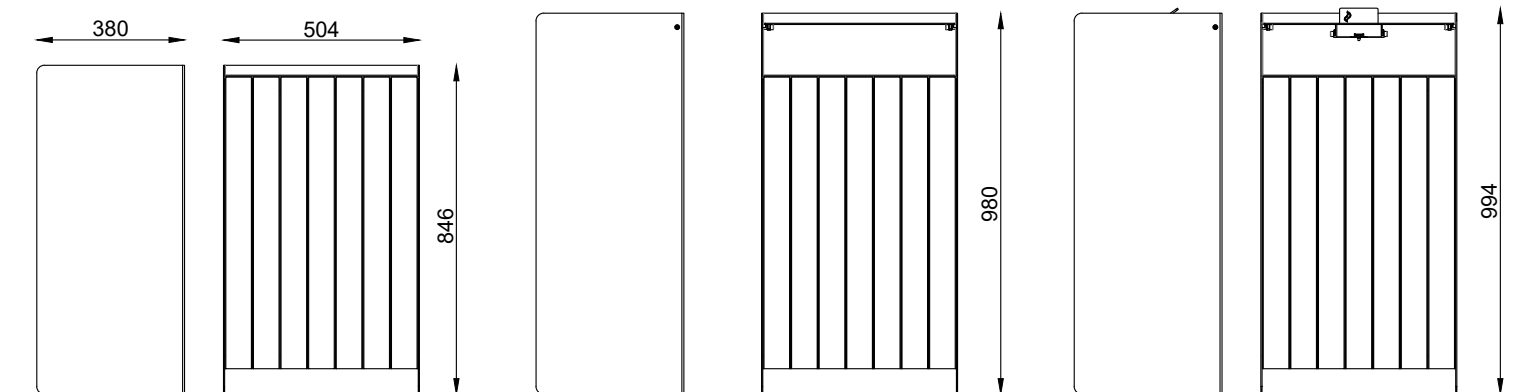
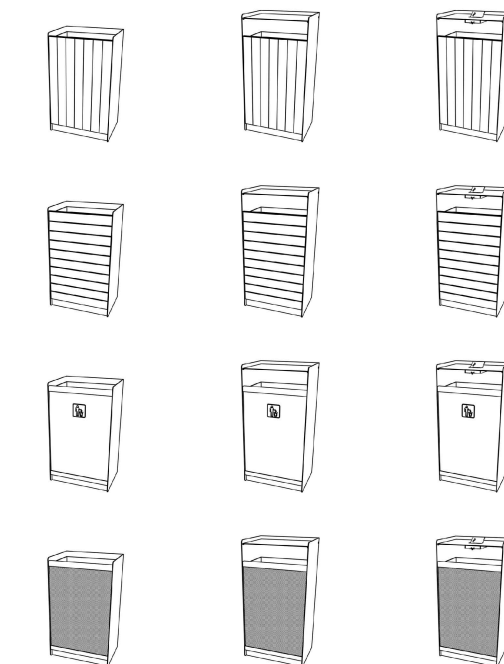
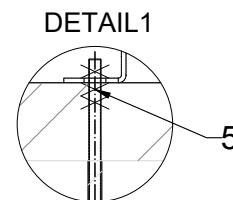
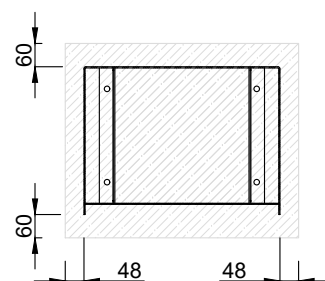


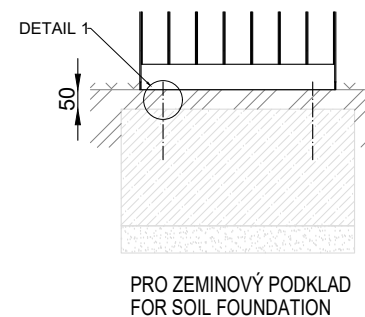

0.09 m3
beton C 12/15
concrete C 12/15

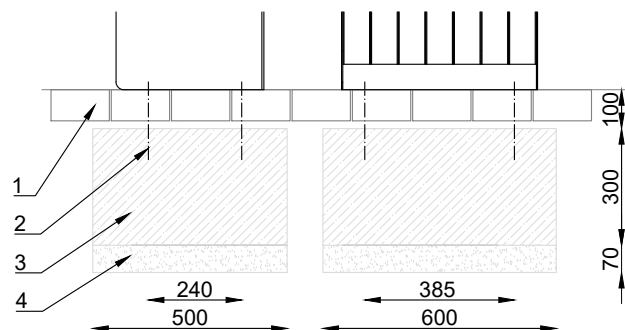

LEGENDA:

- 1 Dlažba
- 2 Chemická kotva M10, dl. min 200 mm
- 3 Betonový základ
- 4 Štěrkové lože ztuhnuté, tl. min. 70 mm
- 5 Kontramatice (pro zeminový podklad)

LEGEND:

- 1 Pavement
- 2 Chemical anchor M10, dl. min 200 mm
- 3 Concrete foundation
- 4 Compacted gravel base, depth min. 70 mm
- 5 Counter nuts (for soil foundation)

KMA511 KMA531
KMA512 KMA532
KMA513 KMA533
KMA521 KMA541
KMA522 KMA542
KMA523 KMA543

Všechna práva vyhrazena. Chráněno průmyslovým vzorem.
All rights reserved. Protection of industrial design.

Rozměry výrobků, základů a kotvení jsou pouze orientační. Přesné rozměry obdržíte při zpracování nabídky naším obchodním oddělením.
Dimensions of products, foundations and anchors are informative only. The exact dimensions you get with our offer.

STREETPARK

version: 2021/05
streetpark.eu