
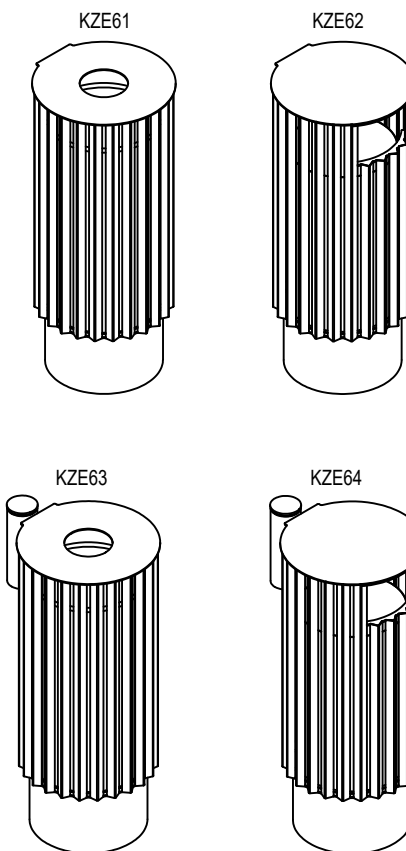


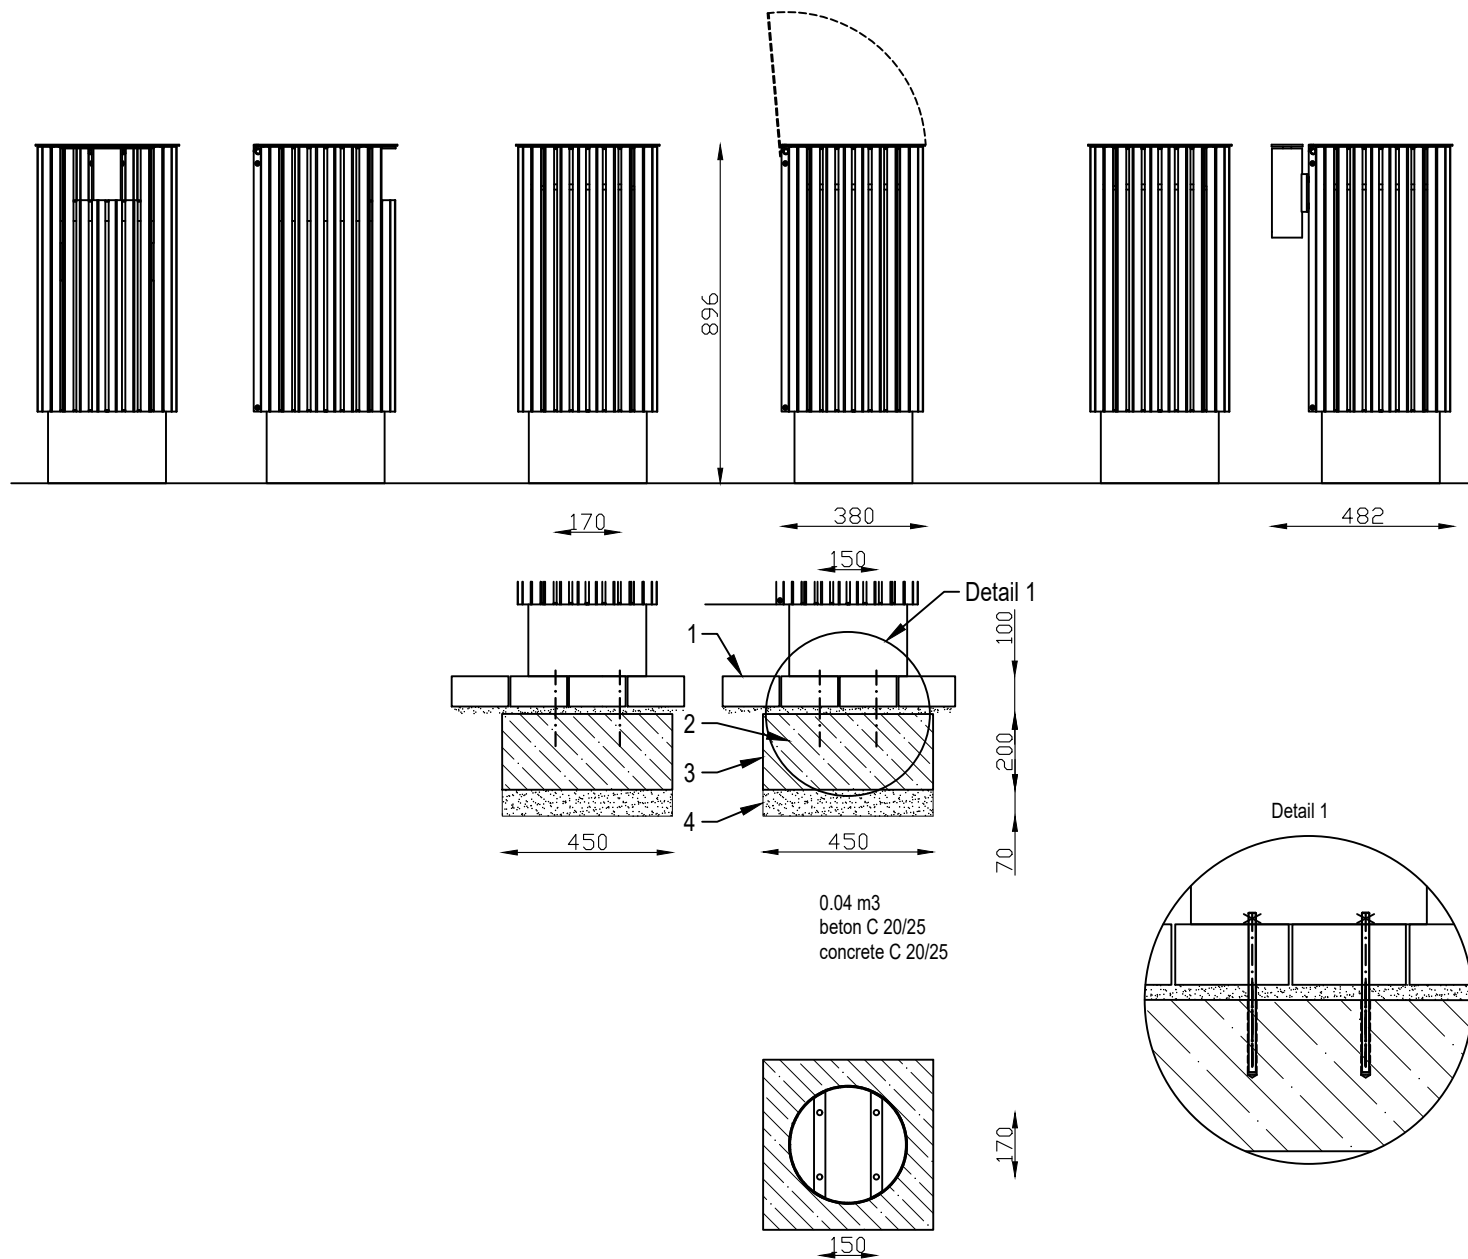

LEGENDA:

- 1 Dlažba
- 2 Chemická kotva M10, dl. min 100
- 3 Betonový základ
- 4 Štěrkové lože zhutněné, tl. min. 70 mm

LEGEND:

- 1 Pavement
- 2 Chemical anchor M10, dl. min 100
- 3 Concrete foundation
- 4 Compacted gravel base, depth min. 70 mm

KZE61 50 l

KZE62 40 l

KZE63 50 l

KZE64 40 l

STREETPARK

Všechna práva vyhrazena. Chráněno průmyslovým vzorem.
All rights reserved. Protection of industrial design.

version: 2025/01
streetpark.eu

Rozměry výrobků, základů a kotvení jsou pouze orientační. Přesné rozměry obdržíte při zpracování nabídky naším obchodním oddělením.
Dimensions of products, foundations and anchors are informative only. The exact dimensions you get with our offer.