
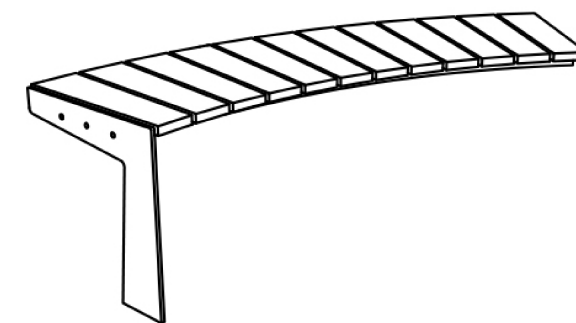
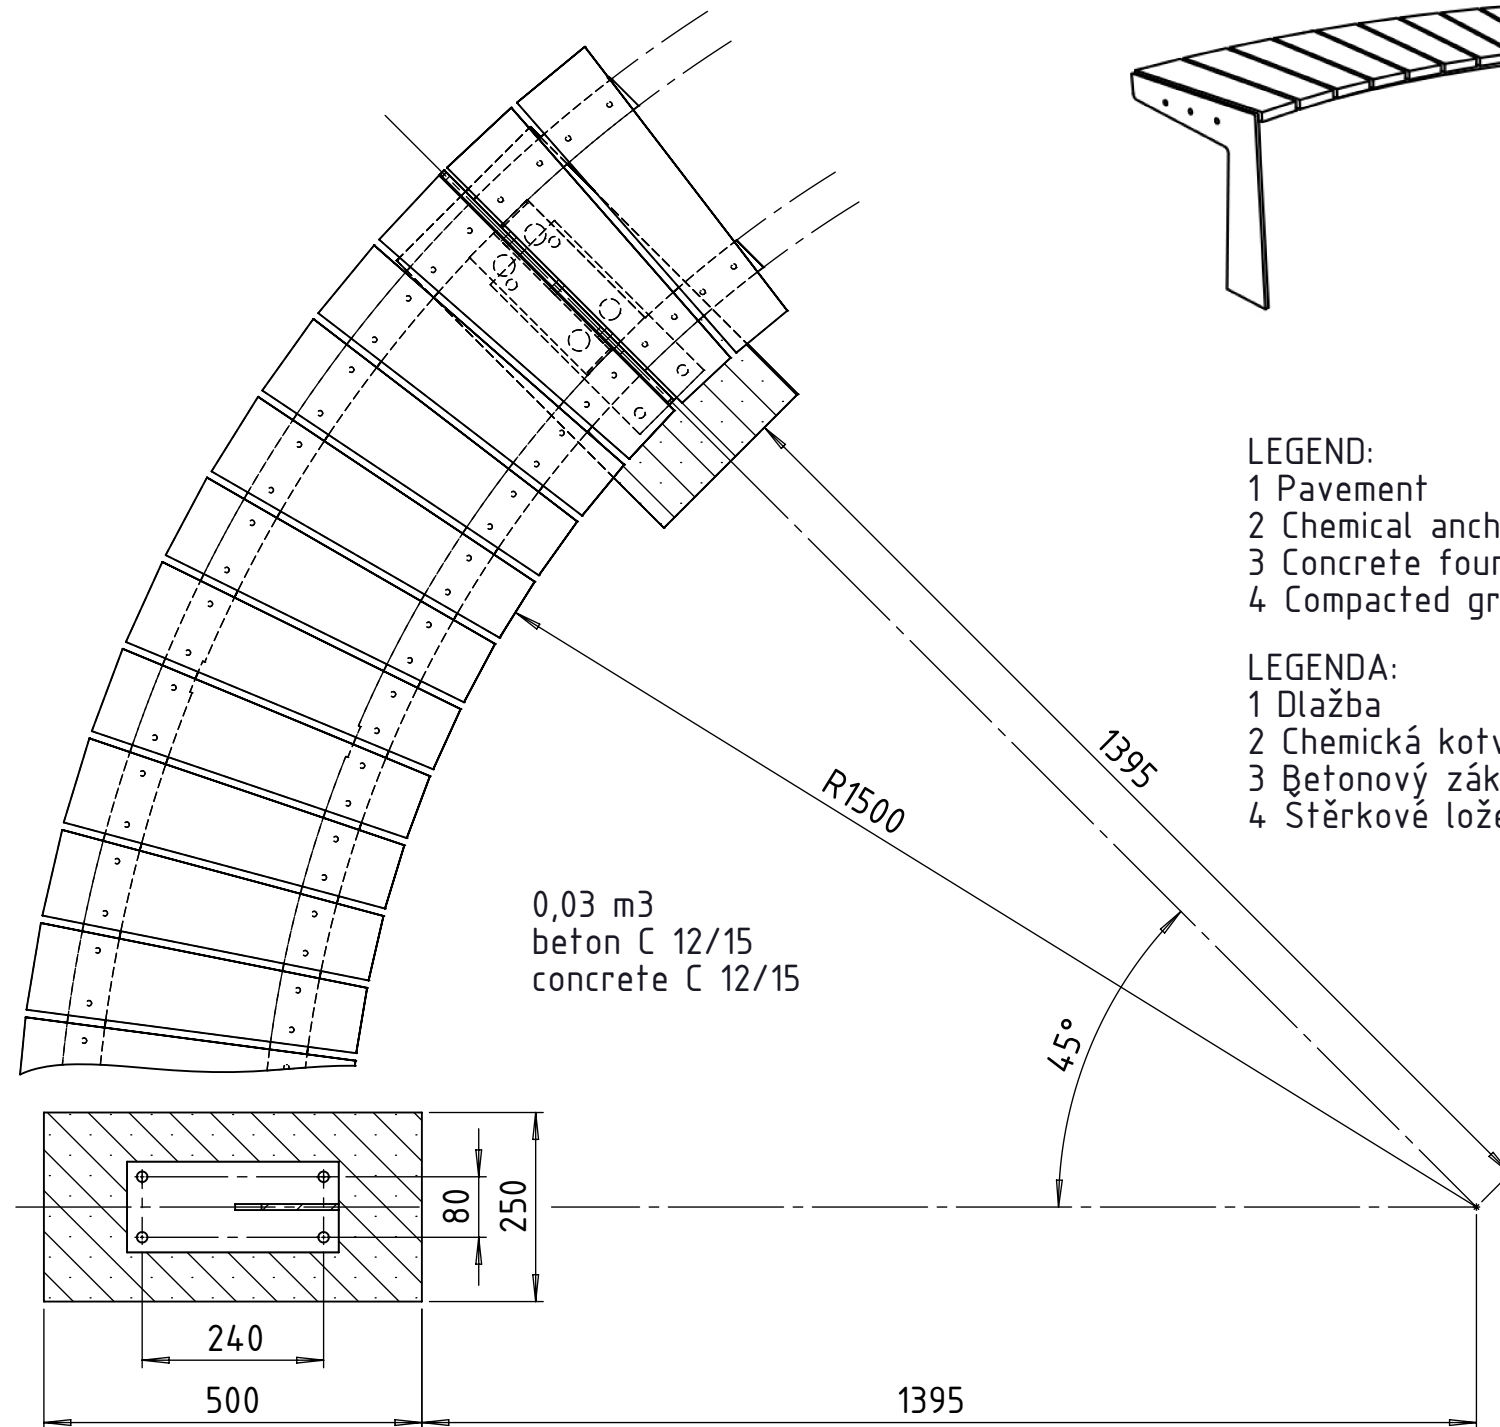
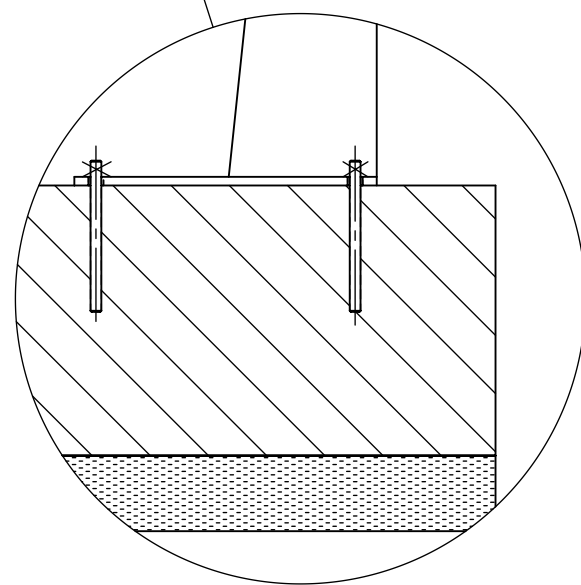
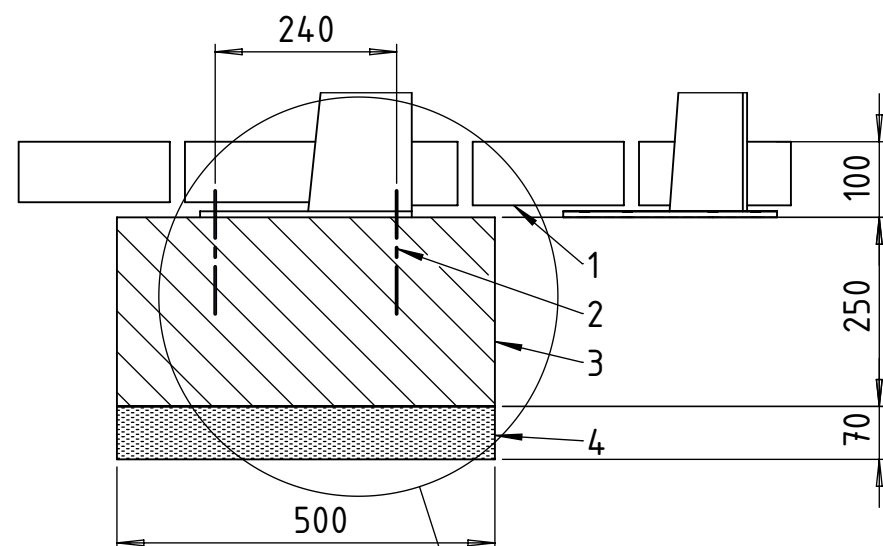


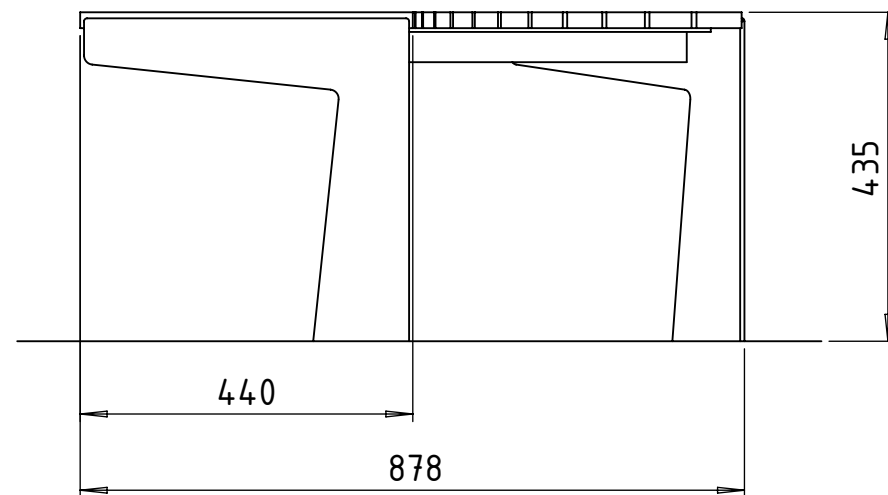

LEGEND:

- 1 Pavement
- 2 Chemical anchor M10, min.length 100mm
- 3 Concrete foundation
- 4 Compacted gravel base, min. depth 70mm

LEGENDA:

- 1 Dlažba
- 2 Chemická kotva M10, min. dl.100mm
- 3 Betonový základ
- 4 Štěrkové lože ztuhněné, tl. min 70mm

Rozměry výrobků a kotvení jsou pouze orientační. Přesné rozměry obdržíte před objednáním naším obchodním oddělením.
Dimensions of product, foundations and anchors are informative only. The exact dimension you get before ordering.

LRA11 R1500mm

STREETPARK

Všechna práva vyhrazena.
Chráněné prům. vzorem.
All rights reserved.
Protection in industrial design.

version: 2019/01
streetpark.eu