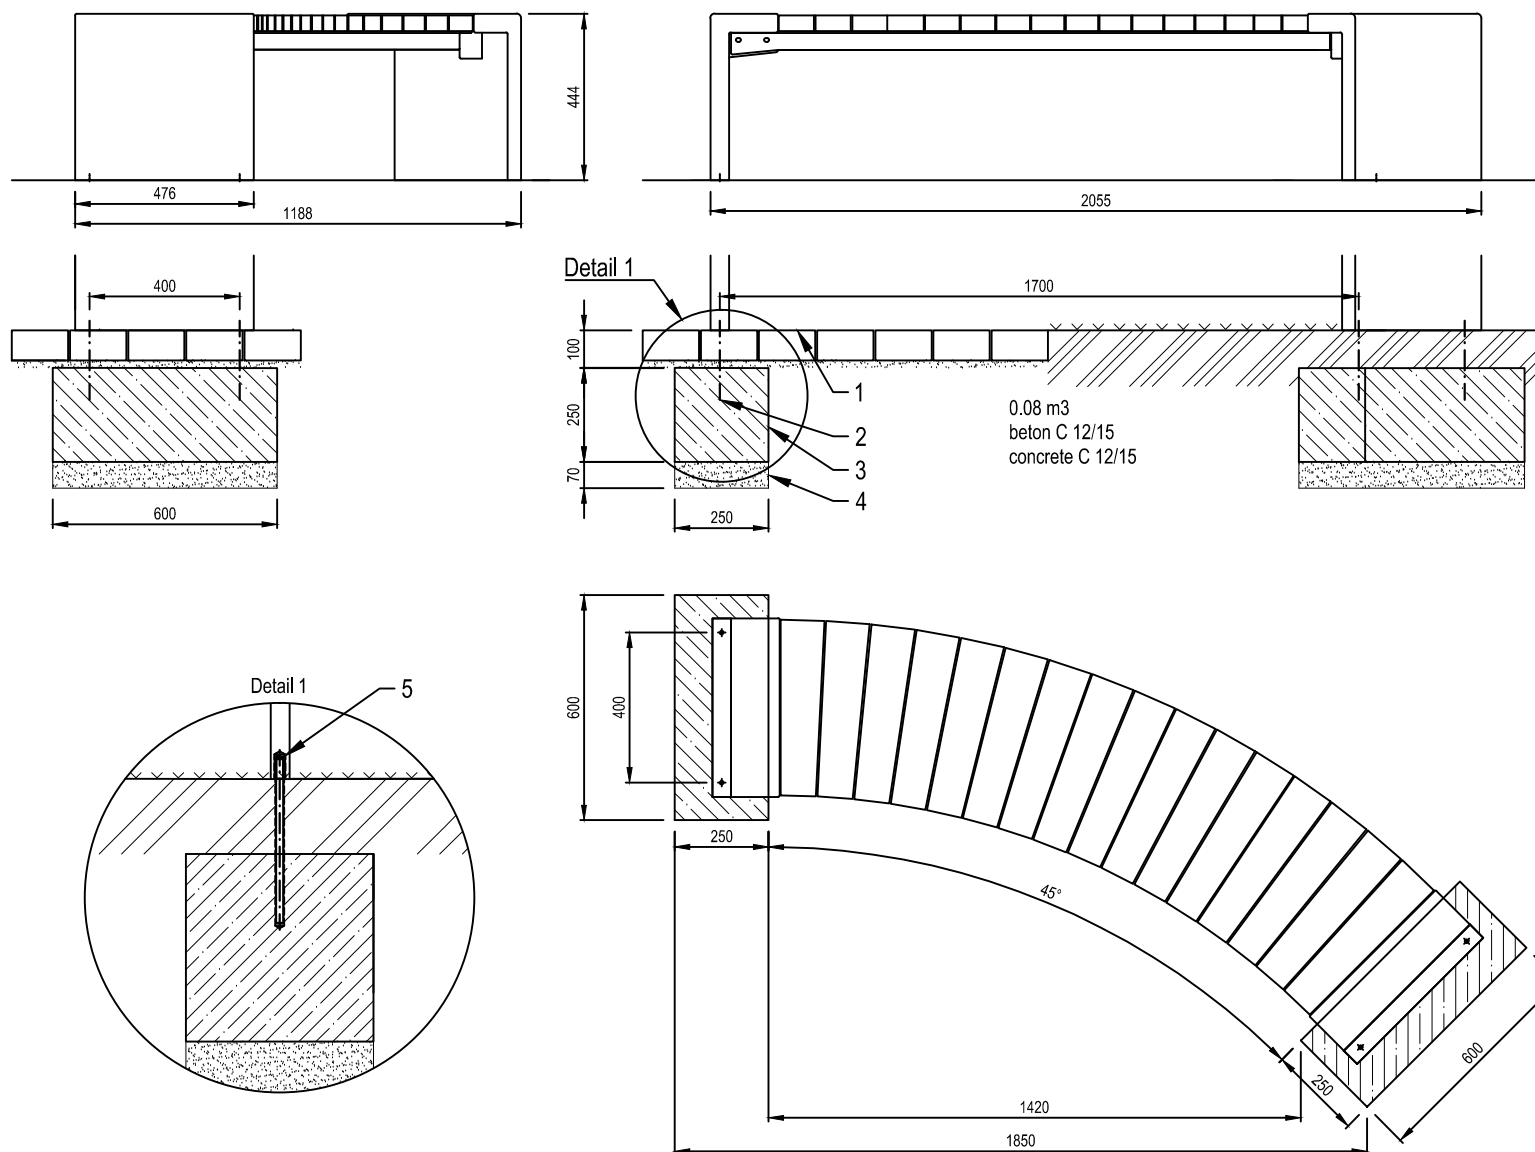


LEGENDA:

- 1 Dlažba
- 2 Chemická kotva M10, dl. min 200
- 3 Betonový základ
- 4 Štěrkové lože ztuhlé, tl. min. 70 mm
- 5 Trubková matice

LEGEND:

- 1 Pavement
- 2 Chemical anchor M10, dl. min 200
- 3 Concrete foundation
- 4 Compacted gravel base, depth min. 70 mm
- 5 Round long nut

Rozměry výrobků, základů a kotvení jsou pouze orientační. Přesné rozměry obdržíte při zpracování nabídky naším obchodním oddělením.
Dimensions of products, foundations and anchors are informative only. The exact dimensions you get with our offer.

LSI9 R2000 mm

STREETPARK

Všechna práva vyhrazena. Chráněno průmyslovým vzorem.
All rights reserved. Protection of industrial design.

version: 2018/01
streetpark.eu