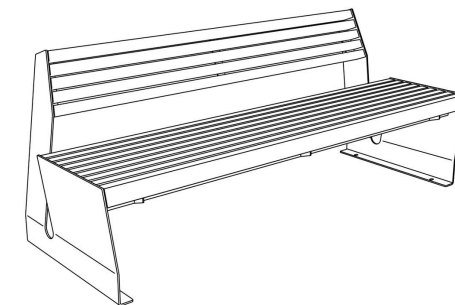
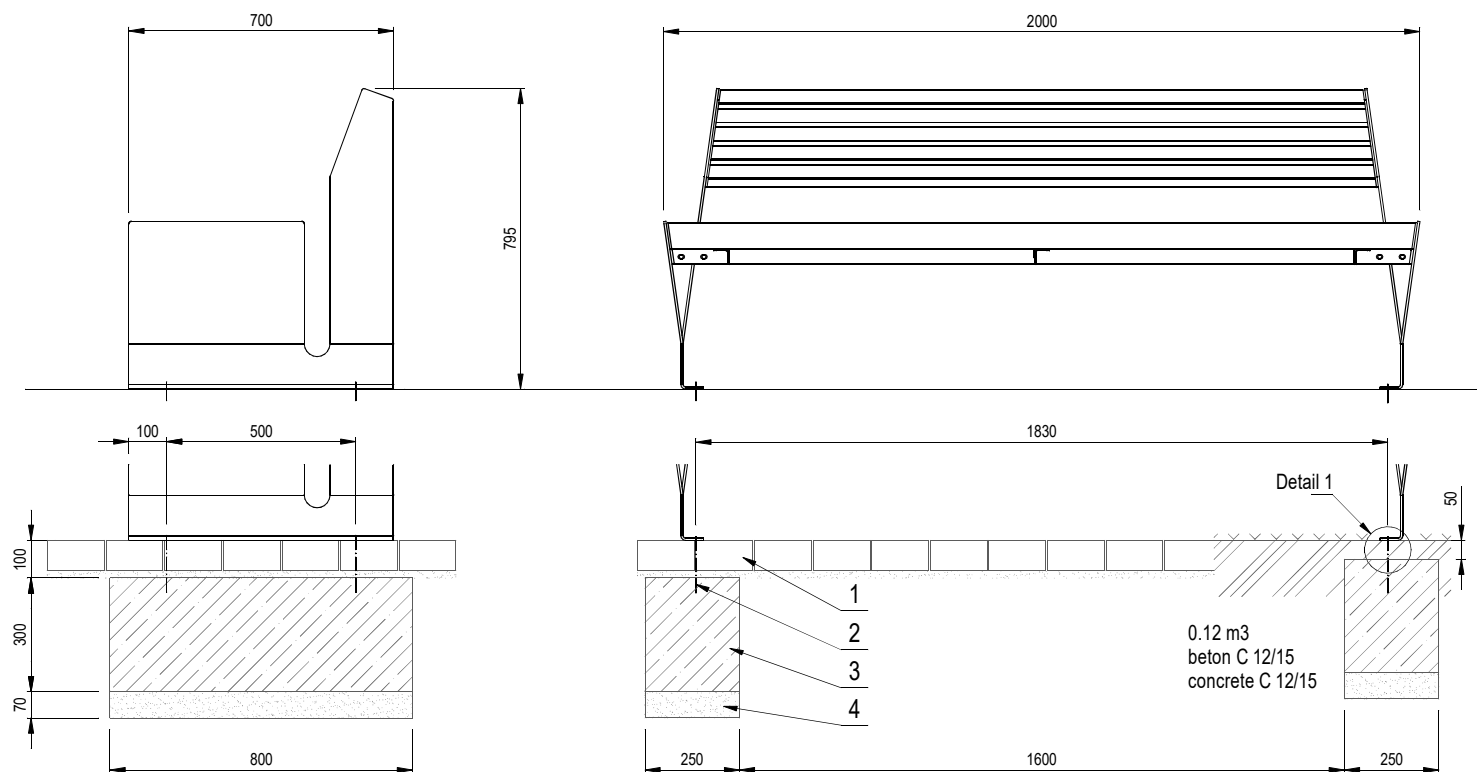


LEGENDA:

- 1 Dlažba
- 2 Chemická kotva M10, dl. min 100
- 3 Betonový základ
- 4 Štěrkové lože zhuťněné, tl. min. 70 mm
- 5 Kontramatice (pro zeminový podklad)

LEGEND:

- 1 Pavement
- 2 Chemical anchor M10, dl. min 100
- 3 Concrete foundation
- 4 Compacted gravel base, depth min. 70 mm
- 5 Counter nuts (for soil foundation)

Rozměry výrobků, základů a kotvení jsou pouze orientační. Přesné rozměry obdržíte při zpracování nabídky naším obchodním oddělením.
Dimensions of products, foundations and anchors are informative only. The exact dimensions you get with our offer.

LVG120

Všedna práva vyhrazena. Chráněno průmyslovým vzorem.
All rights reserved. Protection of industrial design.

STREETPARK

version: 2021/02
streetpark.eu