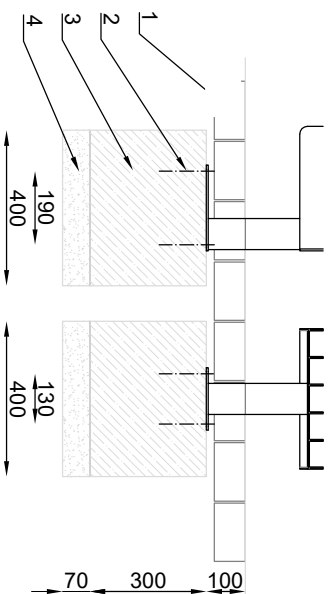
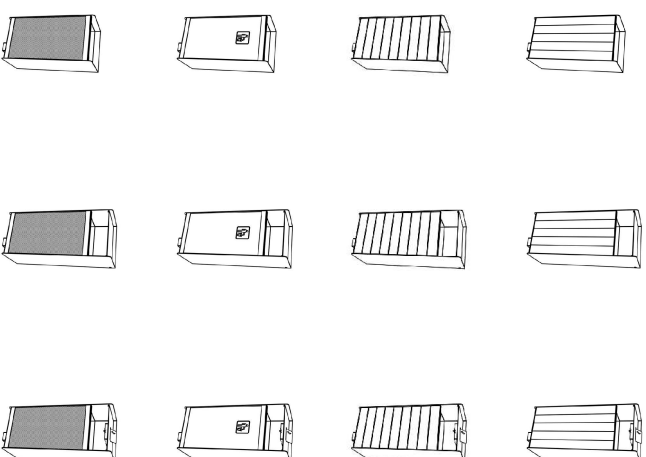
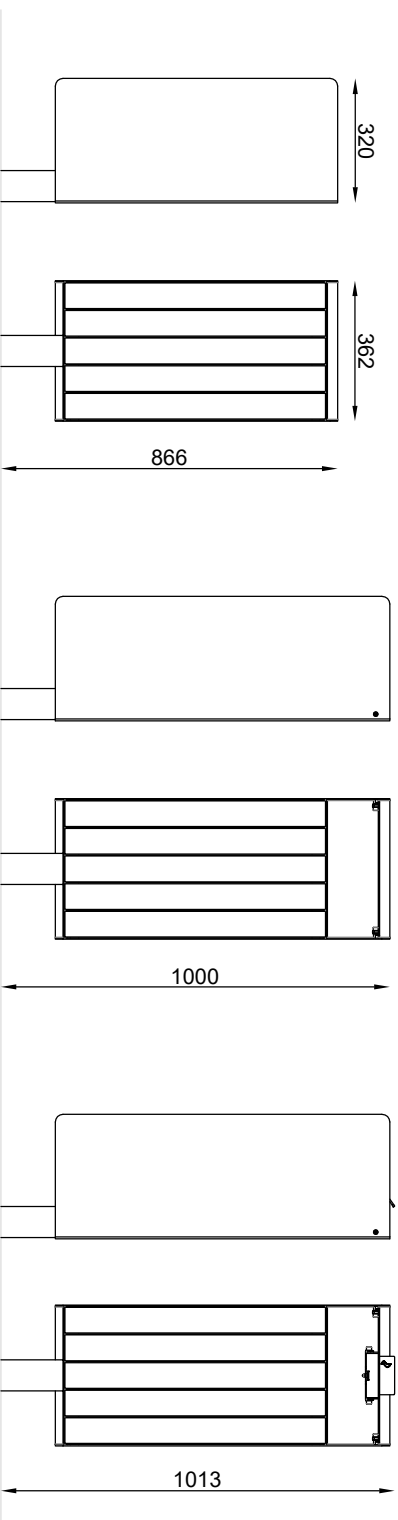


LEGEND:

- 1 Pavement
- 2 Chemical anchor M10, dl. min 100
- 3 Concrete foundation
- 4 Compacted gravel base, depth min. 70 mm

KMA111 KMA131
KMA112 KMA132
KMA113 KMA133
KMA121 KMA141
KMA122 KMA142
KMA123 KMA143

Dimensions of products, fundations and anchors are informative only. The exact dimensions you get with our offer.