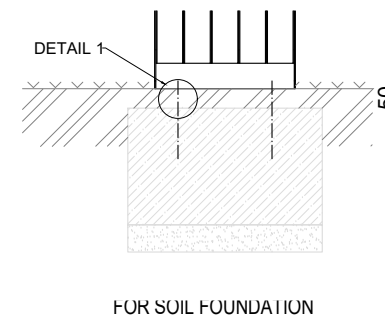
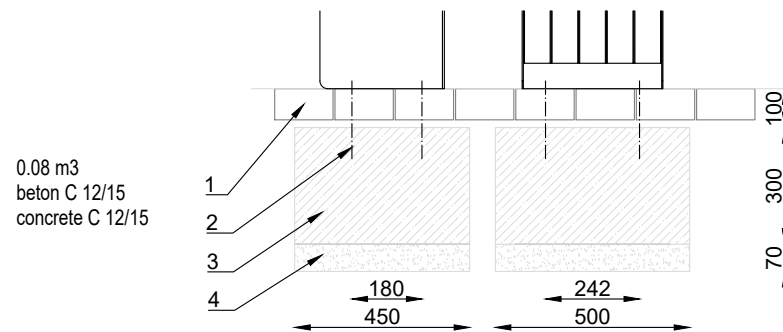
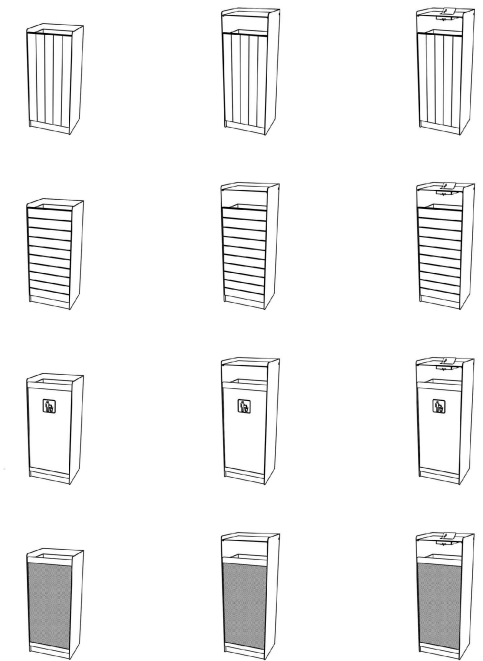
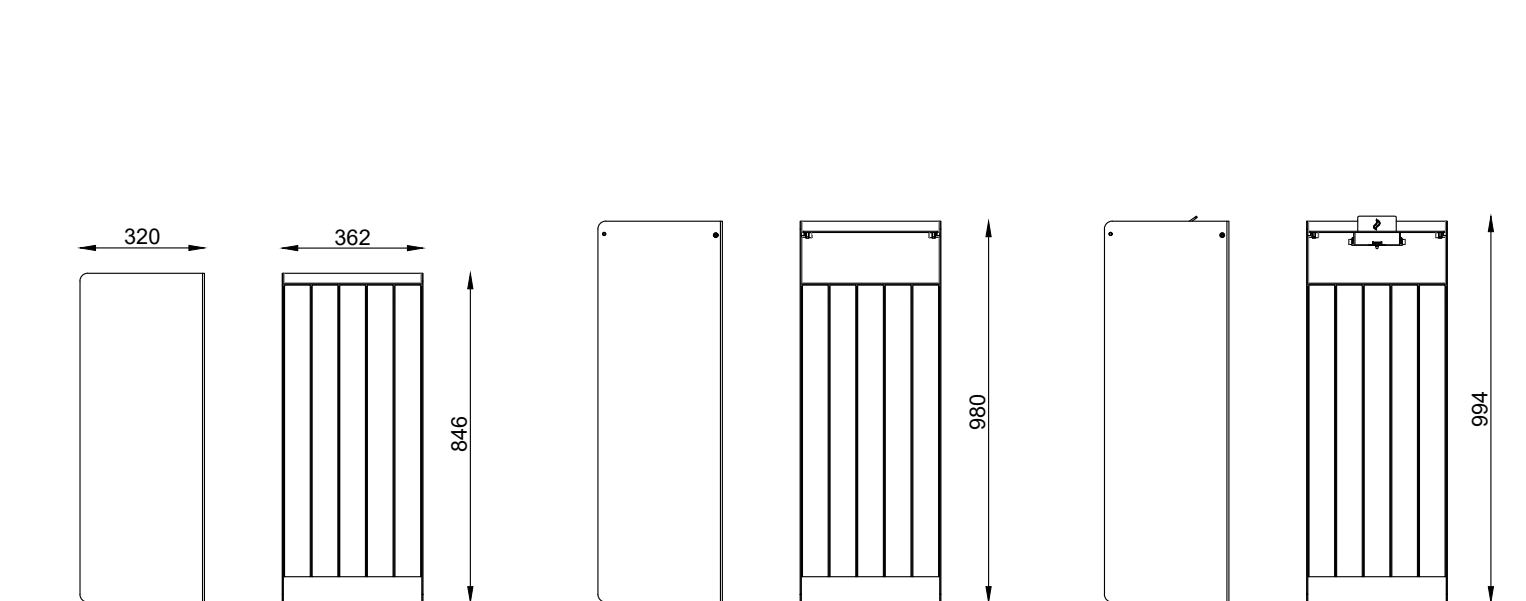


LEGEND:
1 Pavement
2 Chemical anchor M10, dl. min 200 mm
3 Concrete foundation
4 Compacted gravel base, depth min. 70 mm
5 Counter nuts (for soil foundation)

KMA211 KMA231
KMA212 KMA232
KMA213 KMA233
KMA221 KMA241
KMA222 KMA242
KMA223 KMA243