

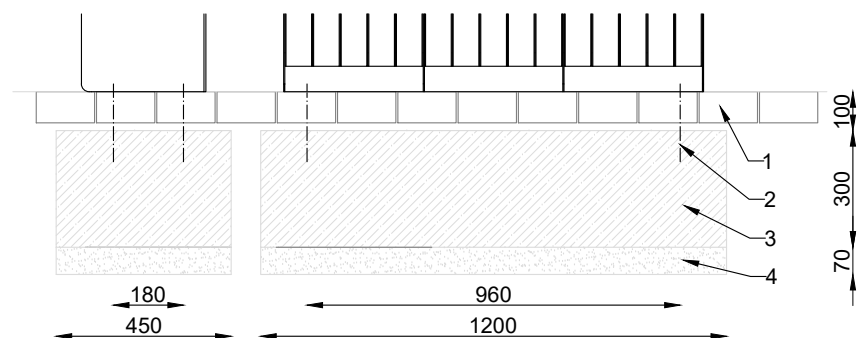
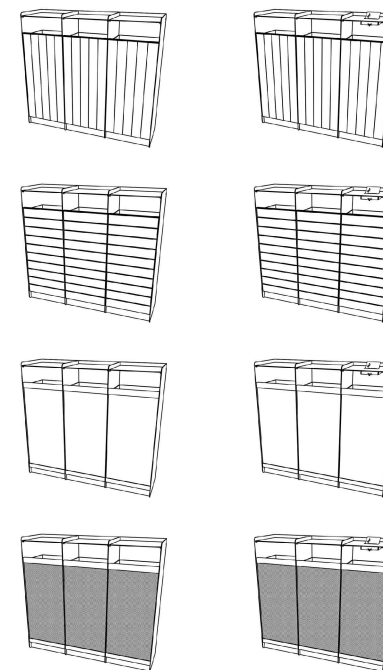
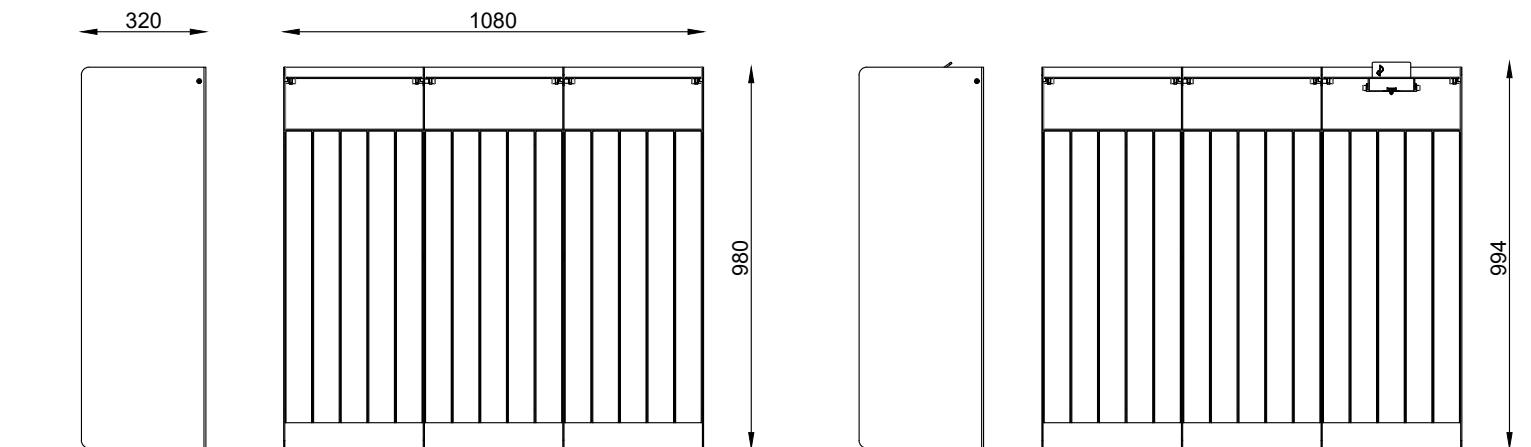


FOR SOIL FOUNDATION

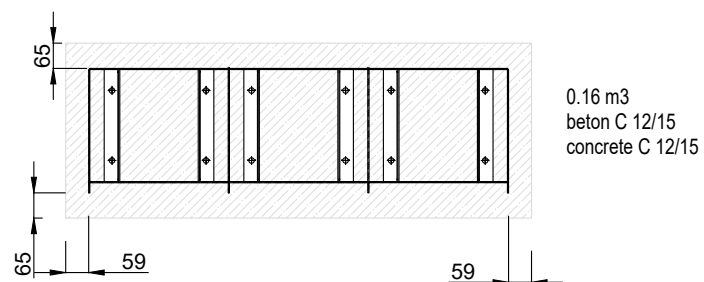

DETAIL1

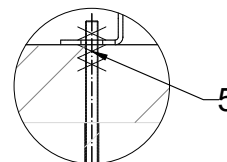

LEGEND:

- 1 Pavement
- 2 Chemical anchor M10, dl. min 200 mm
- 3 Concrete foundation
- 4 Compacted gravel base, depth min. 70 mm
- 5 Counter nuts (for soil foundation)

KMA312 KMA332
KMA313 KMA333
KMA322 KMA342
KMA323 KMA343