
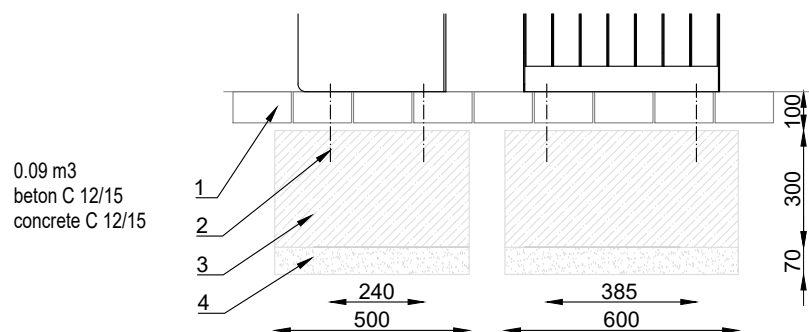
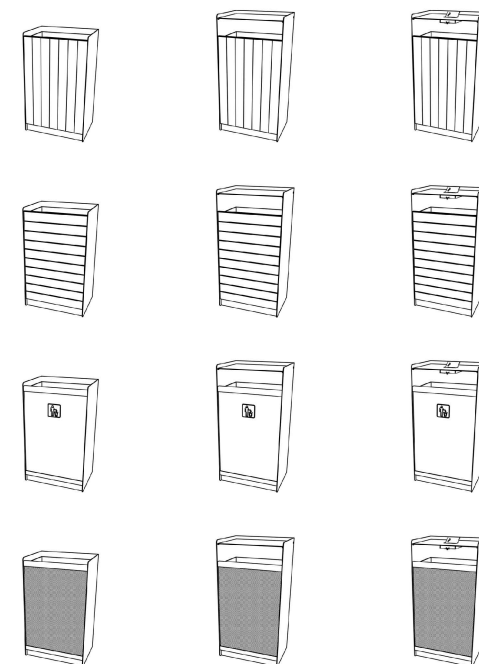
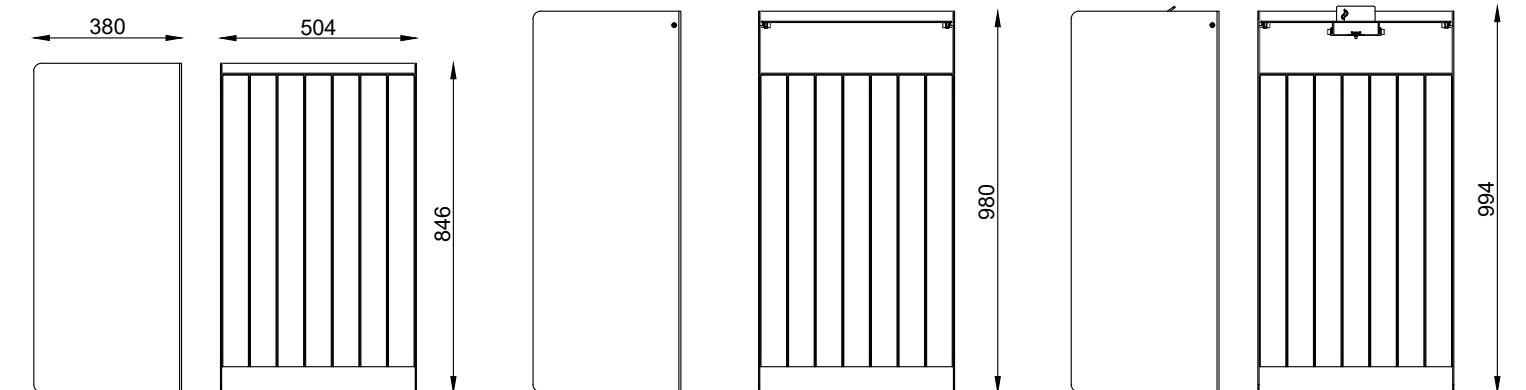
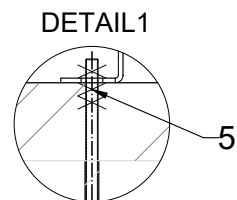


FOR SOIL FOUNDATION

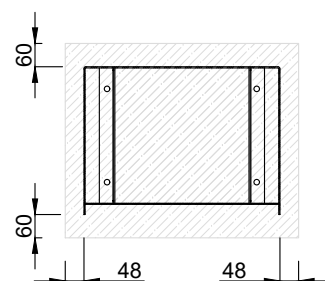

LEGEND:

- 1 Pavement
- 2 Chemical anchor M10, dl. min 200 mm
- 3 Concrete foundation
- 4 Compacted gravel base, depth min. 70 mm
- 5 Counter nuts (for soil foundation)

KMA511 KMA531
KMA512 KMA532
KMA513 KMA533
KMA521 KMA541
KMA522 KMA542
KMA523 KMA543