


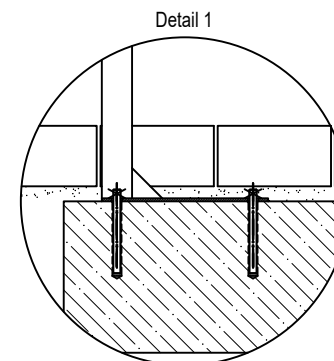
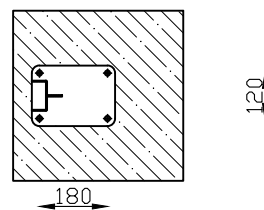


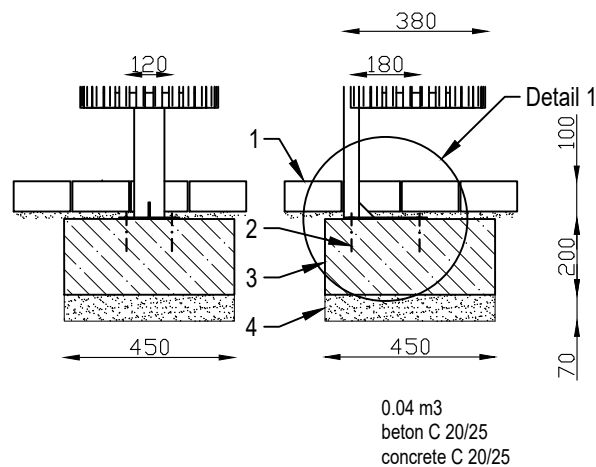


KZE11

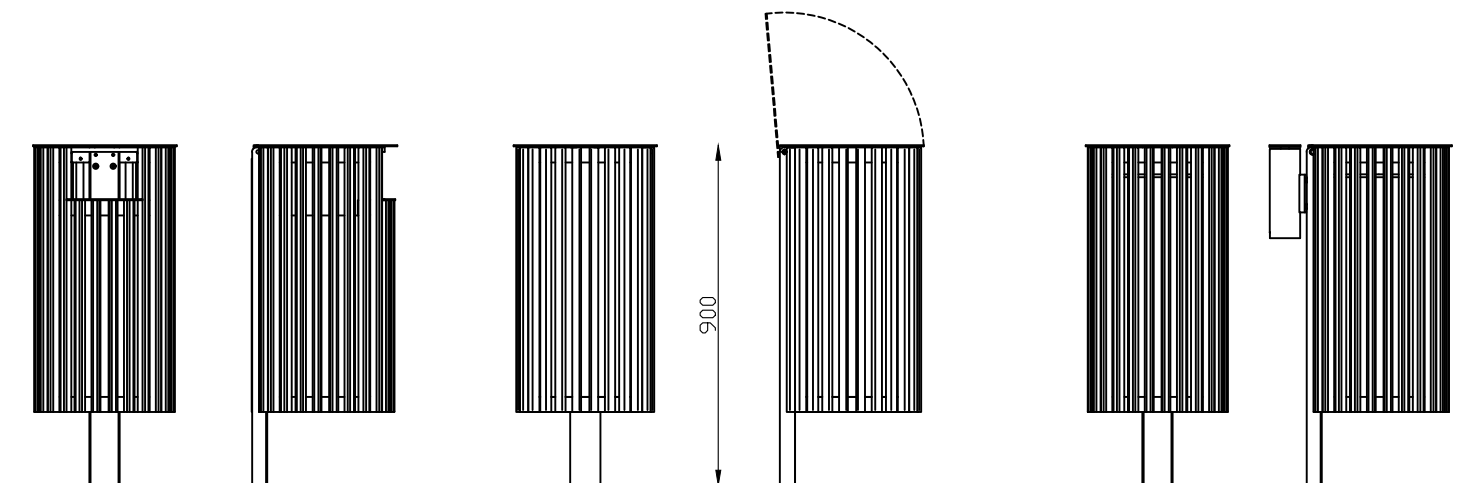


KZE12

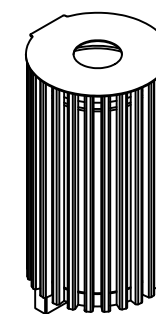

KZE13

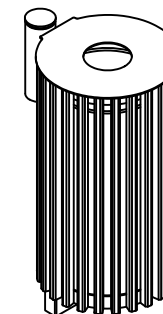

KZE14

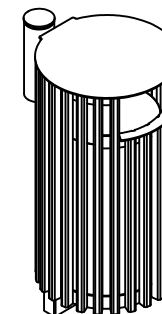

LEGEND:

- 1 Pavement
- 2 Chemical anchor M10, dl. min 100
- 3 Concrete foundation
- 4 Compacted gravel base, depth min. 70 mm

KZE11 45 l

KZE12 35 l

KZE13 45 l

KZE14 35 l