

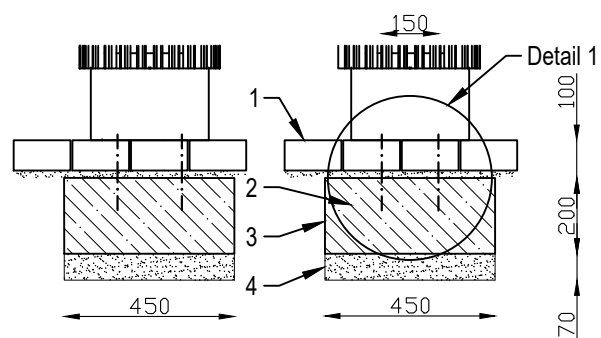
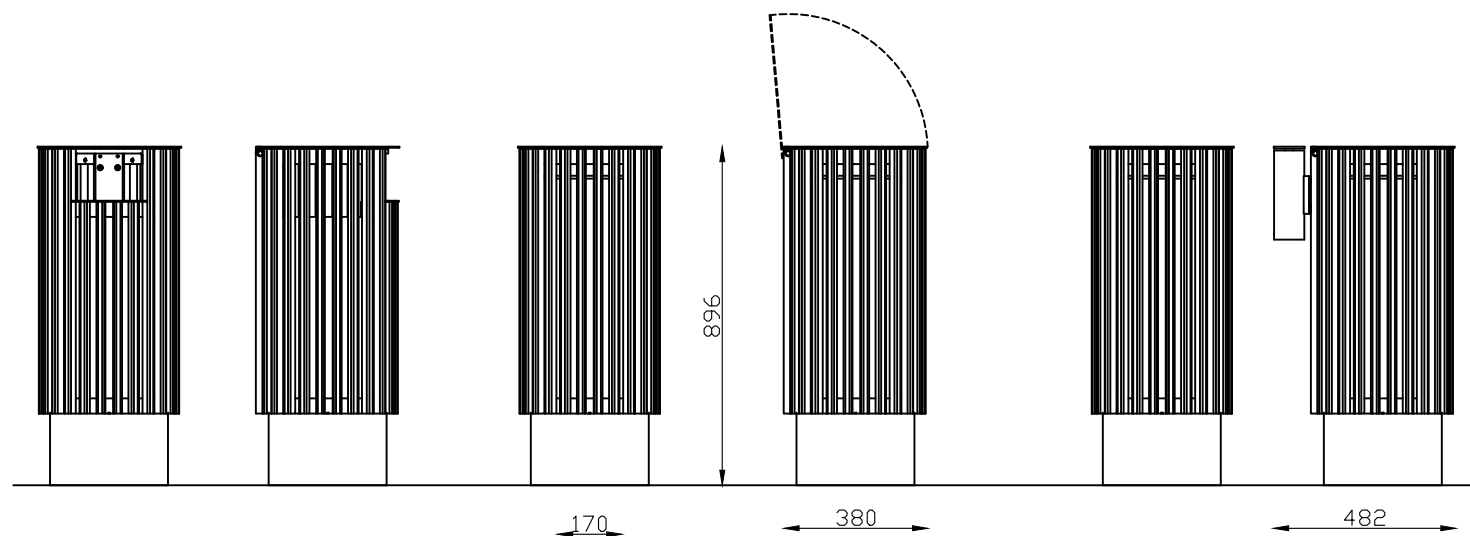


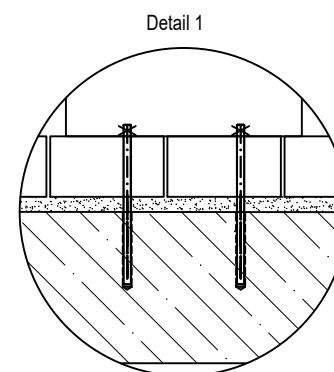

0.04 m3
beton C 20/25
concrete C 20/25

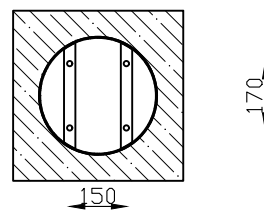

LEGEND:
1 Pavement
2 Chemical anchor M10, dl. min 100
3 Concrete foundation
4 Compacted gravel base, depth min. 70 mm

KZE51 45 l
KZE52 35 l
KZE53 45 l
KZE54 35 l

