
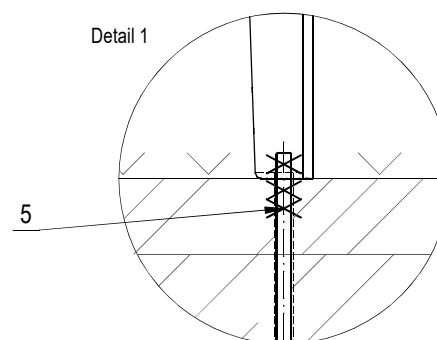
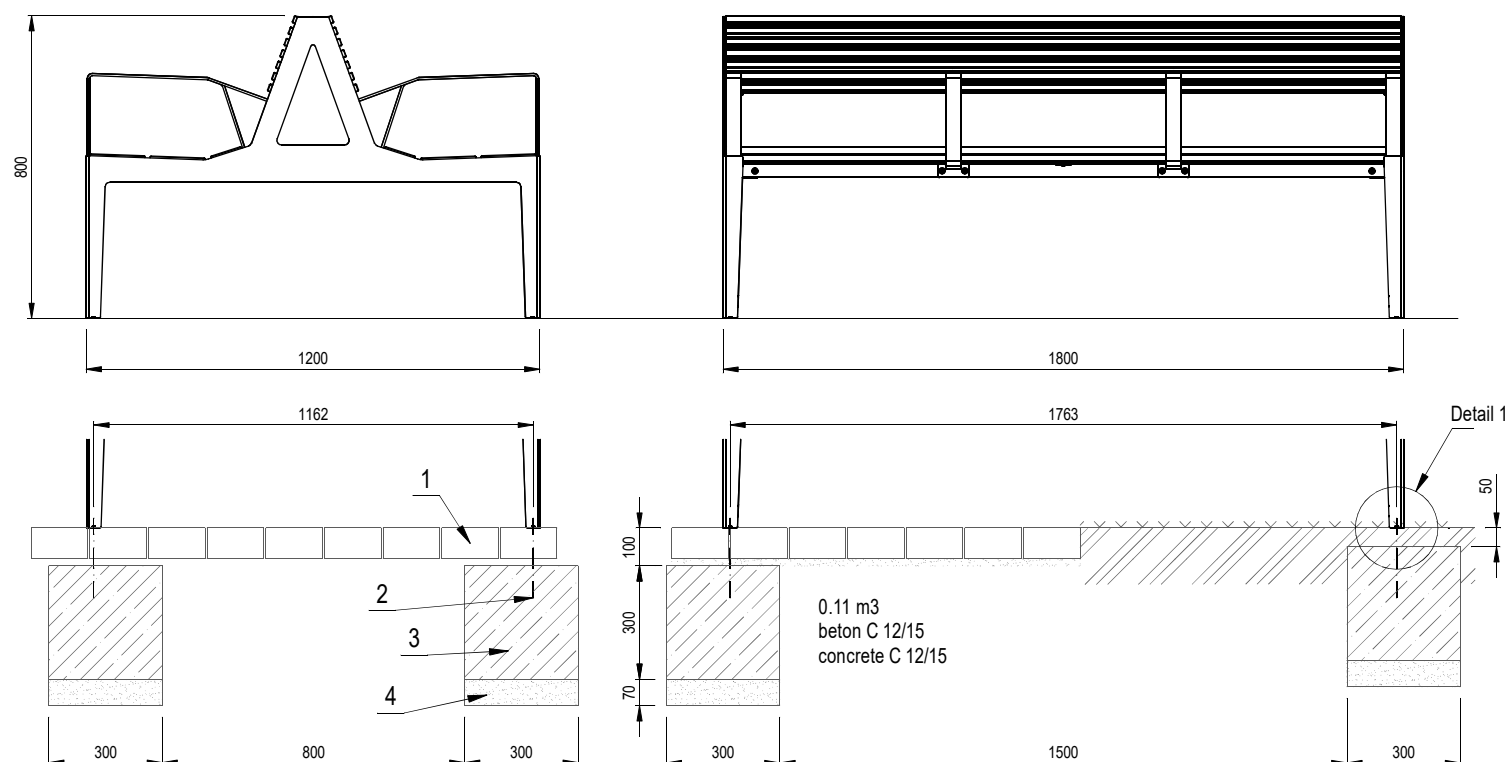
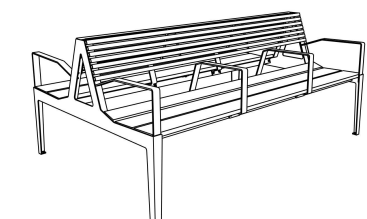
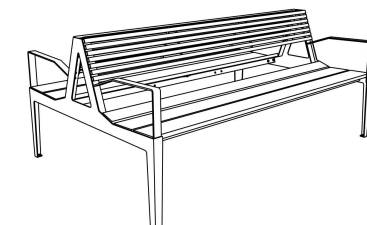


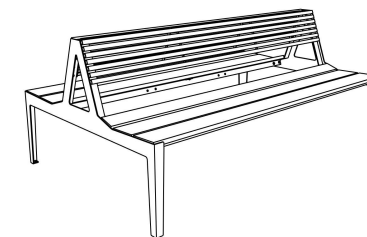

- LEGEND:**
- 1 Pavement
 - 2 Chemical anchor M10, dl. min 200
 - 3 Concrete foundation
 - 4 Compacted gravel base, depth min. 70 mm
 - 5 Counter nuts (for soil foundation)

LBG51
LBG53
LBG55