


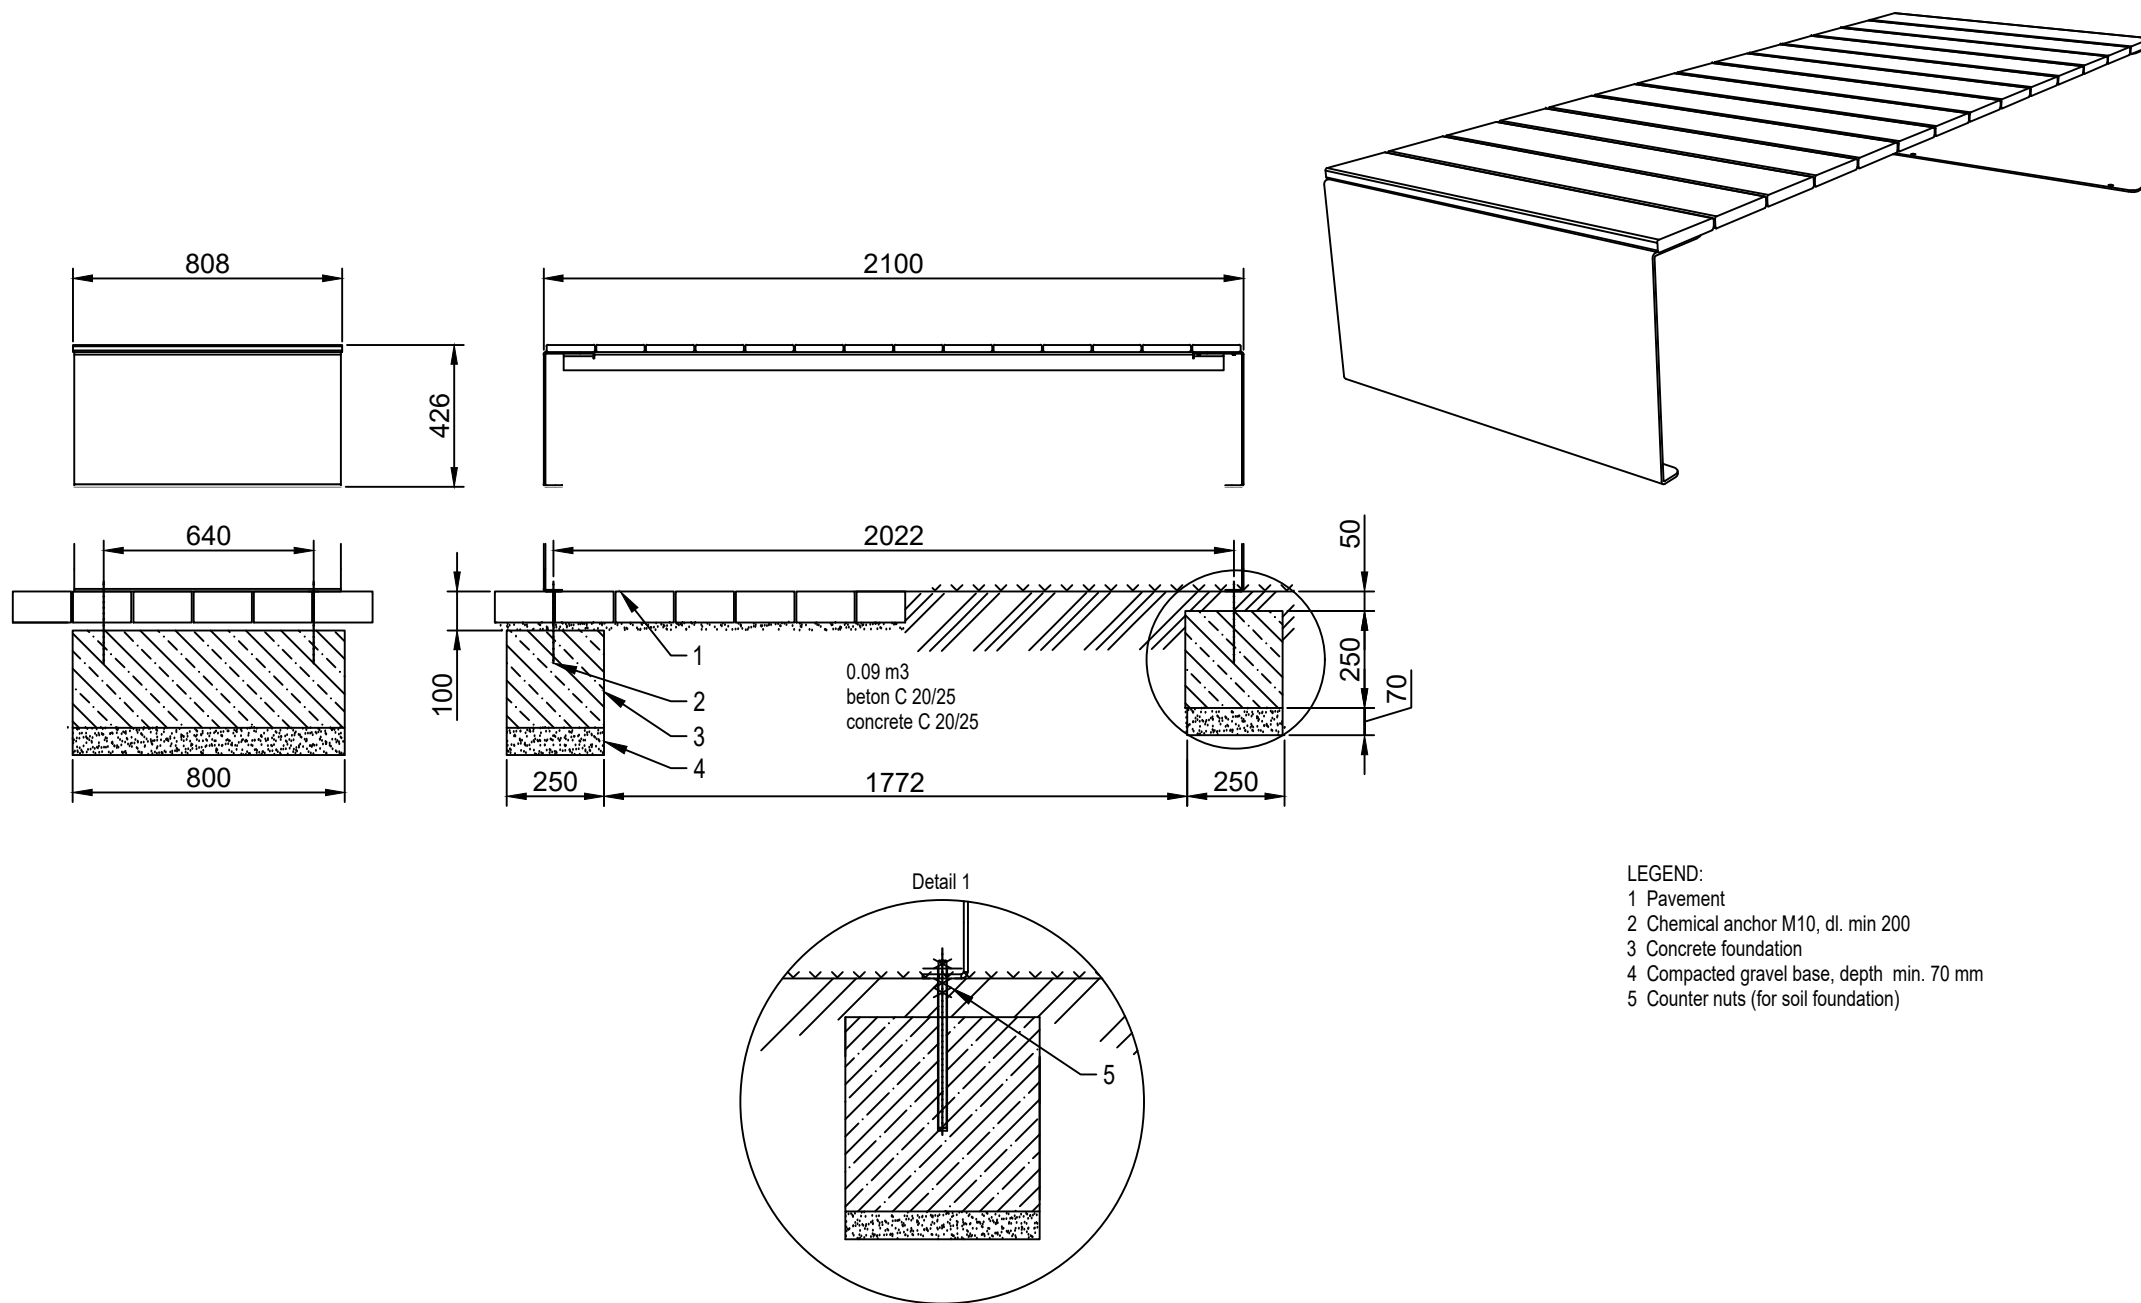

LEGEND:

- 1 Pavement
- 2 Chemical anchor M10, dl. min 200
- 3 Concrete foundation
- 4 Compacted gravel base, depth min. 70 mm
- 5 Counter nuts (for soil foundation)

LFG0LL

Dimensions of products, foundations and anchors are informative only. The exact dimensions you get with our offer.

version: 2026/04