



LGR369 x=640
LGR389 x=824

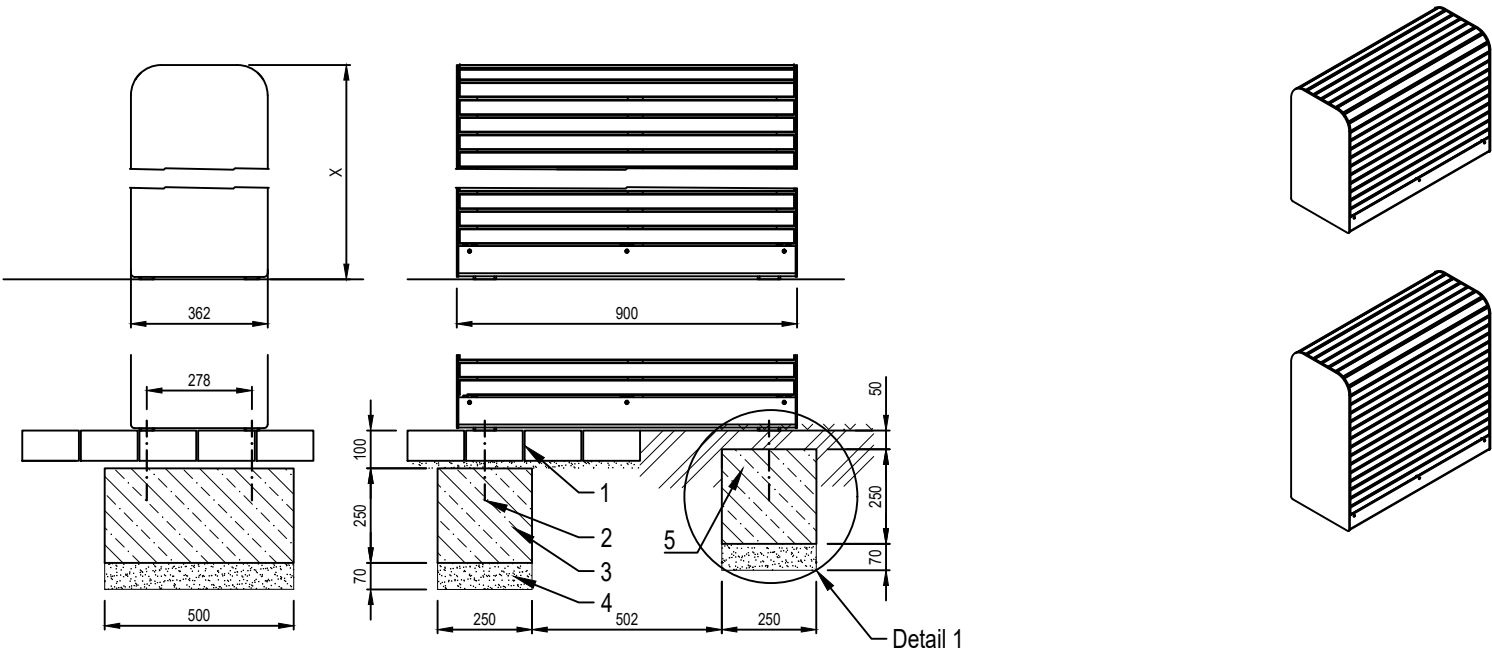

0.07 m3
beton C 20/25
concrete C 20/25

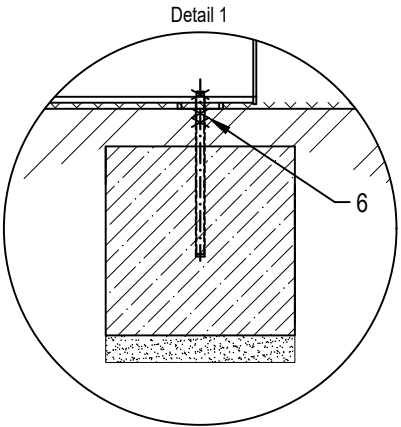

- LEGEND:
- 1 Pavement
 - 2 Chemical anchor M10, dl. min 200
 - 3 Concrete foundation
 - 4 Compacted gravel base, depth min. 70 mm
 - 5 Soil foundation
 - 6 Counter nuts (for soil foundation)

LGR369
LGR389