
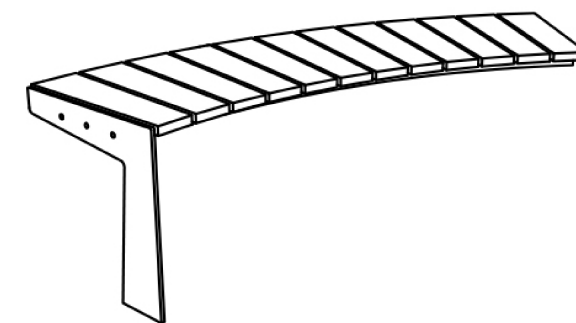
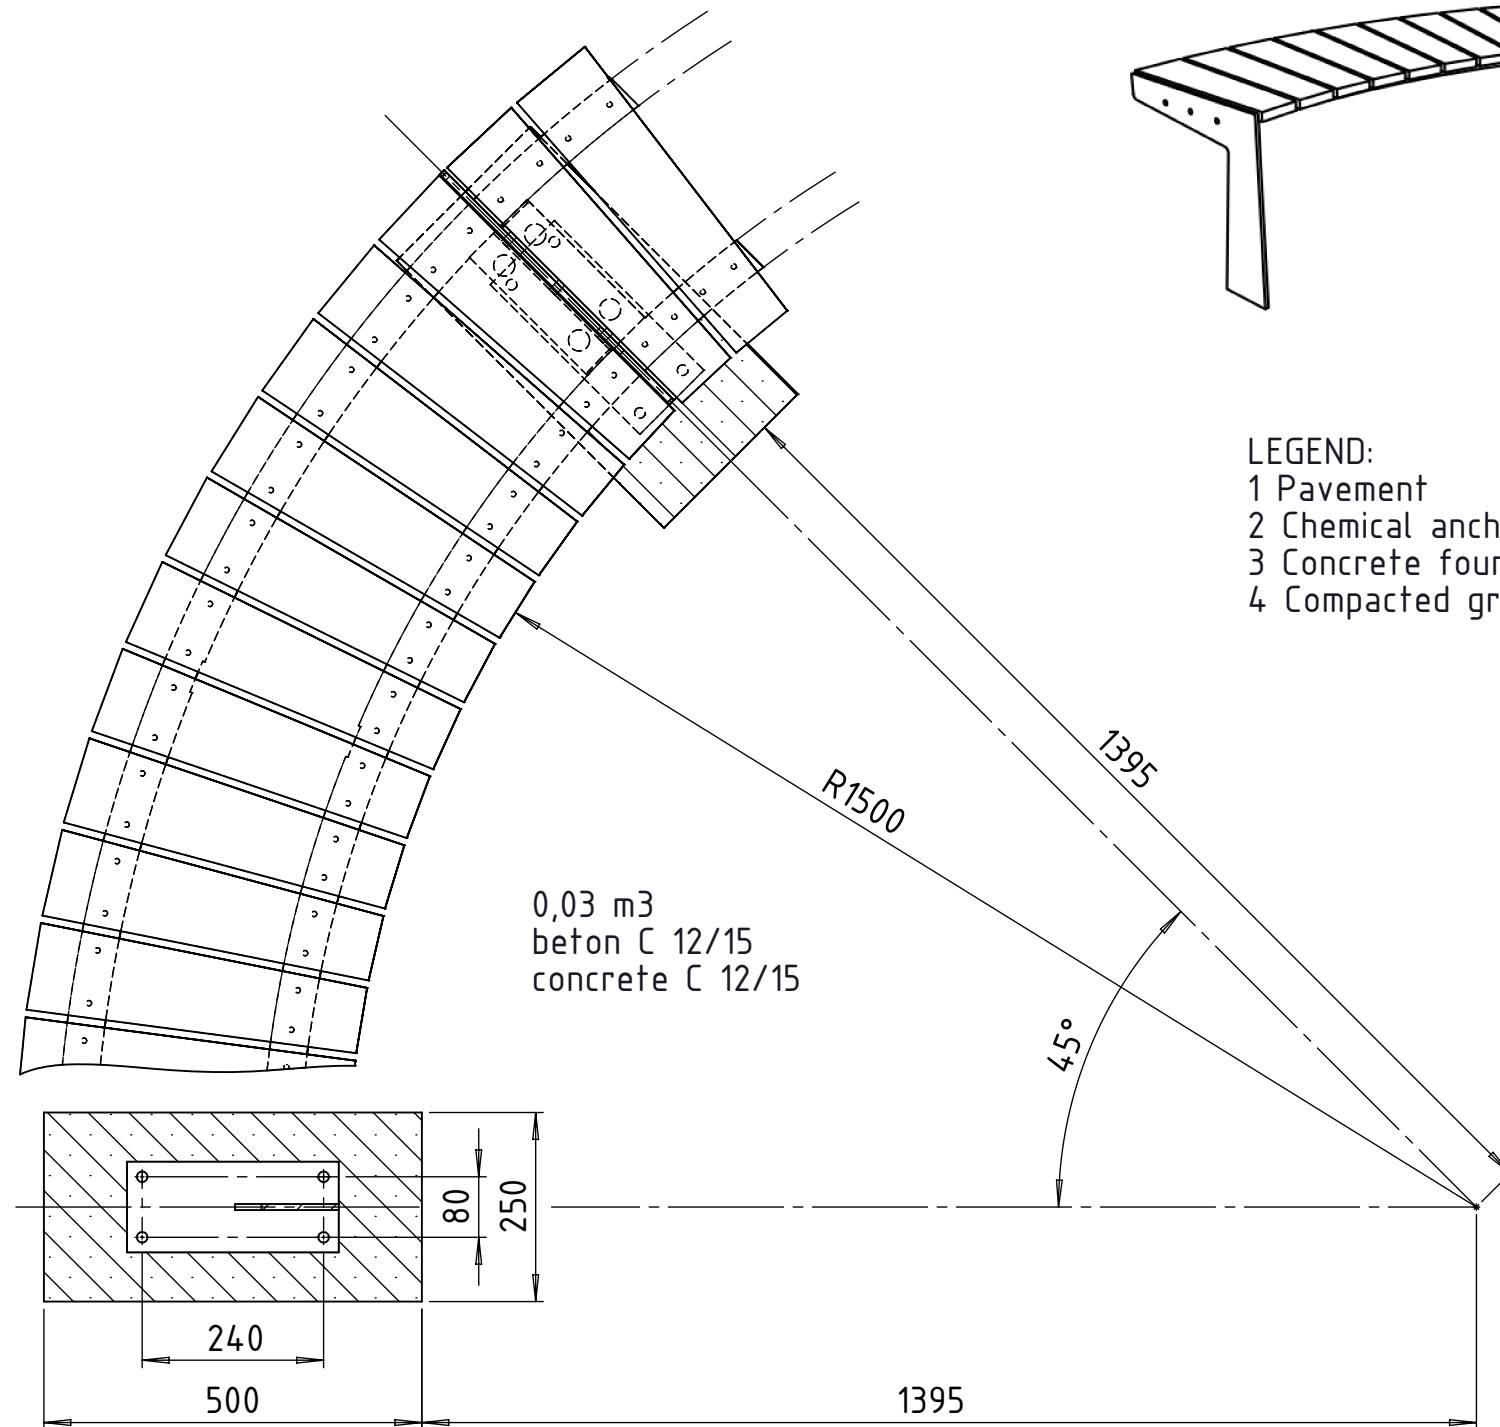
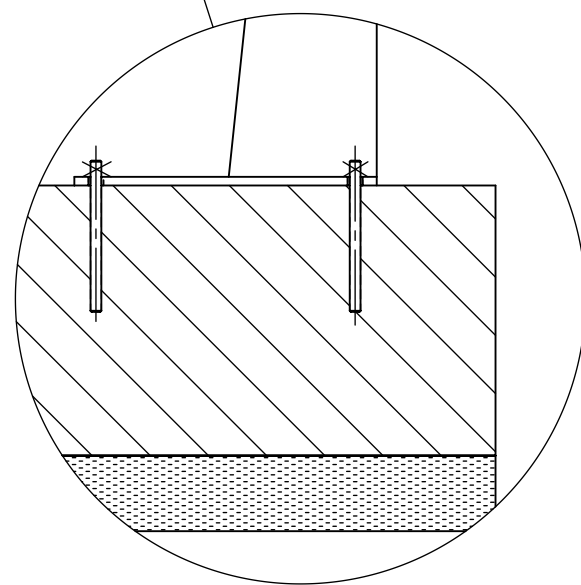
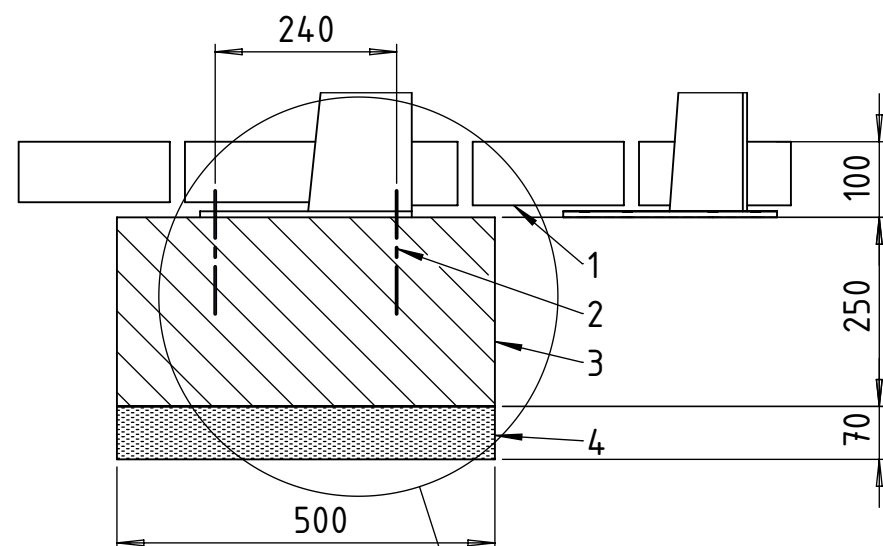


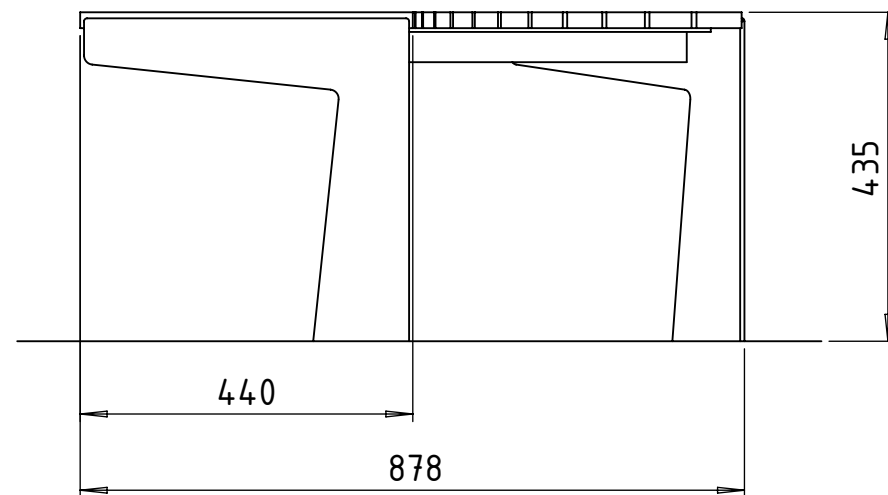

- LEGEND:
- 1 Pavement
 - 2 Chemical anchor M10, min.length 100mm
 - 3 Concrete foundation
 - 4 Compacted gravel base, min. depth 70mm

LRA11 R1500mm