


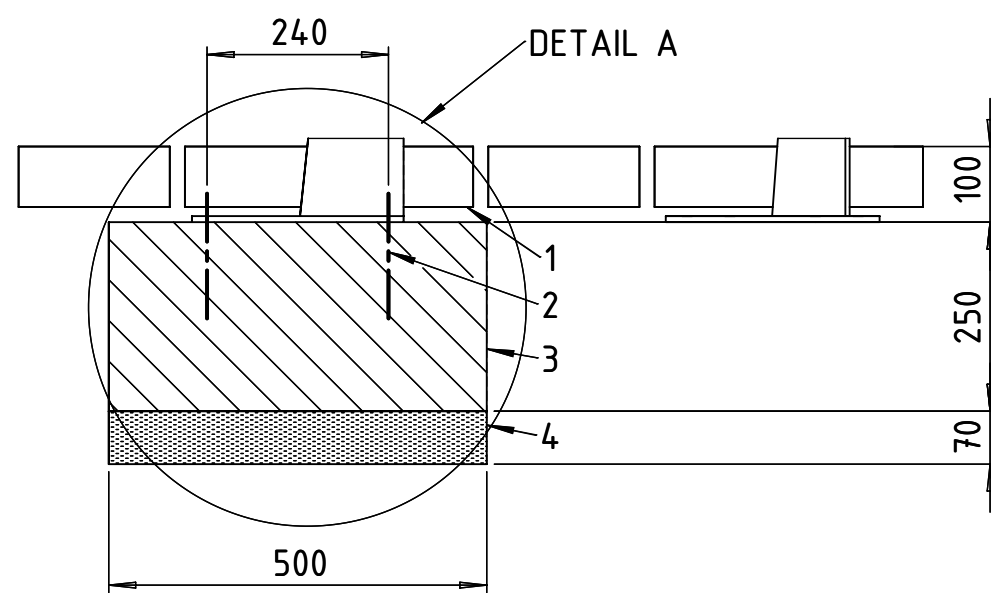
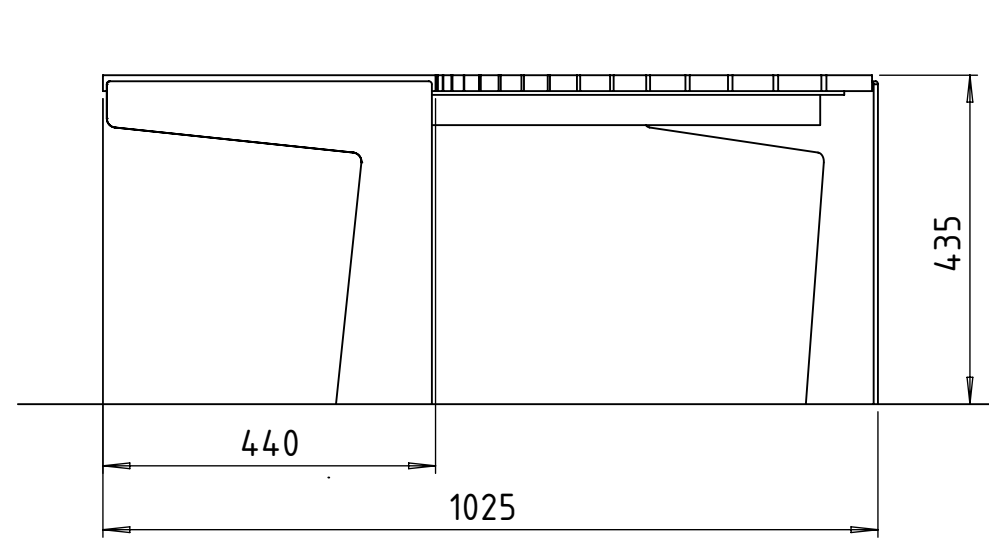
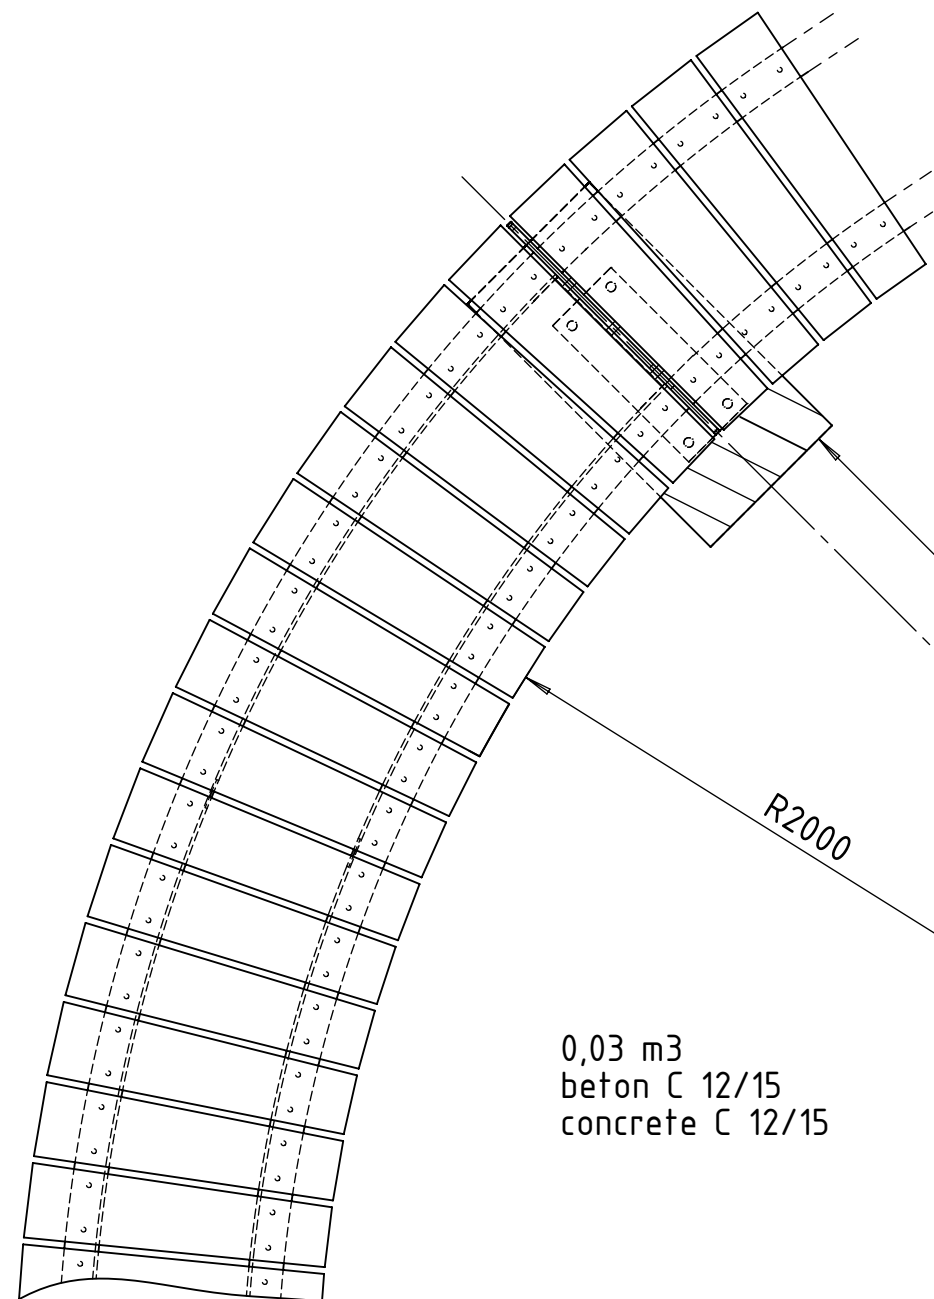


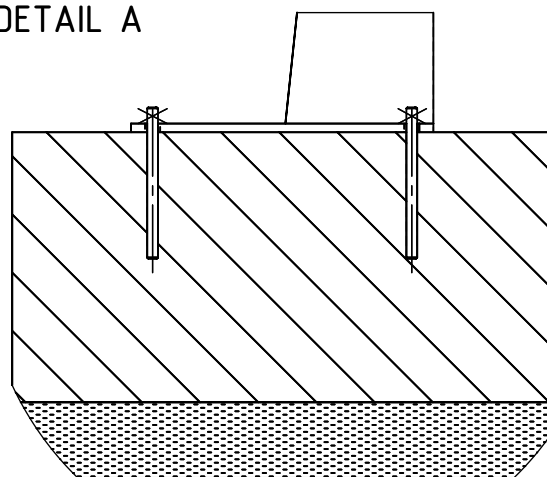

DETAIL A

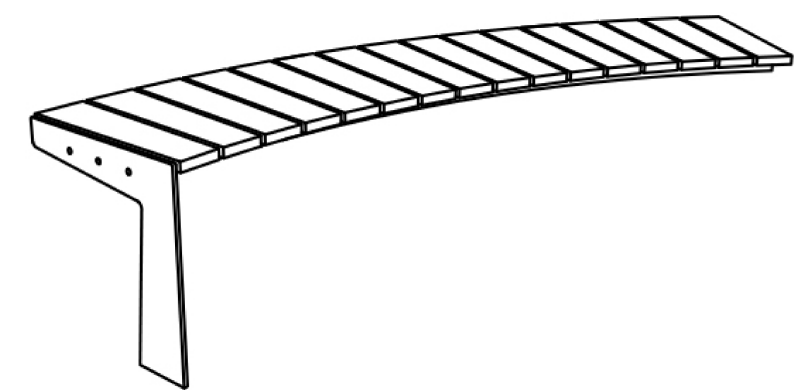


0,03 m3
beton C 12/15
concrete C 12/15

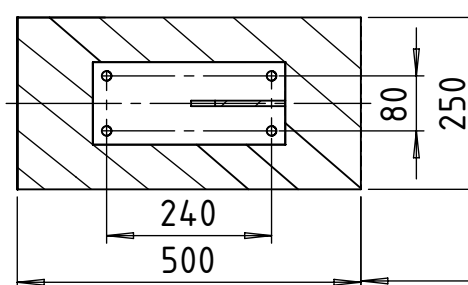

LEGEND:

- 1 Pavement
- 2 Chemical anchor M10, min.length 100mm
- 3 Concrete foundation
- 4 Compacted gravel base, min. depth 70mm

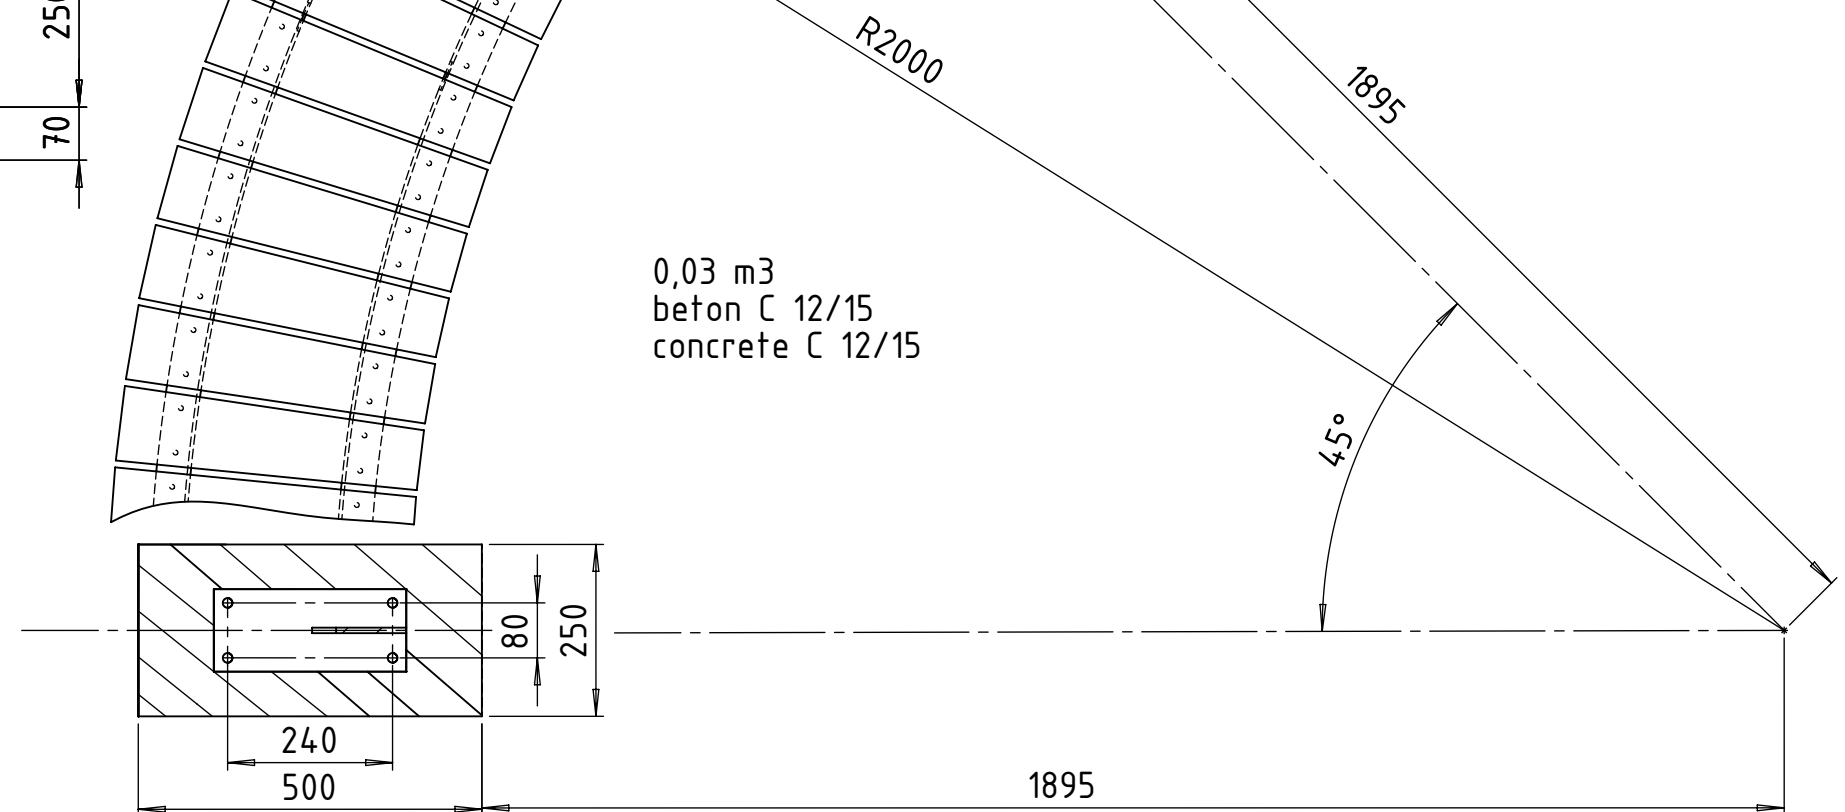

LRA11 R2000mm