
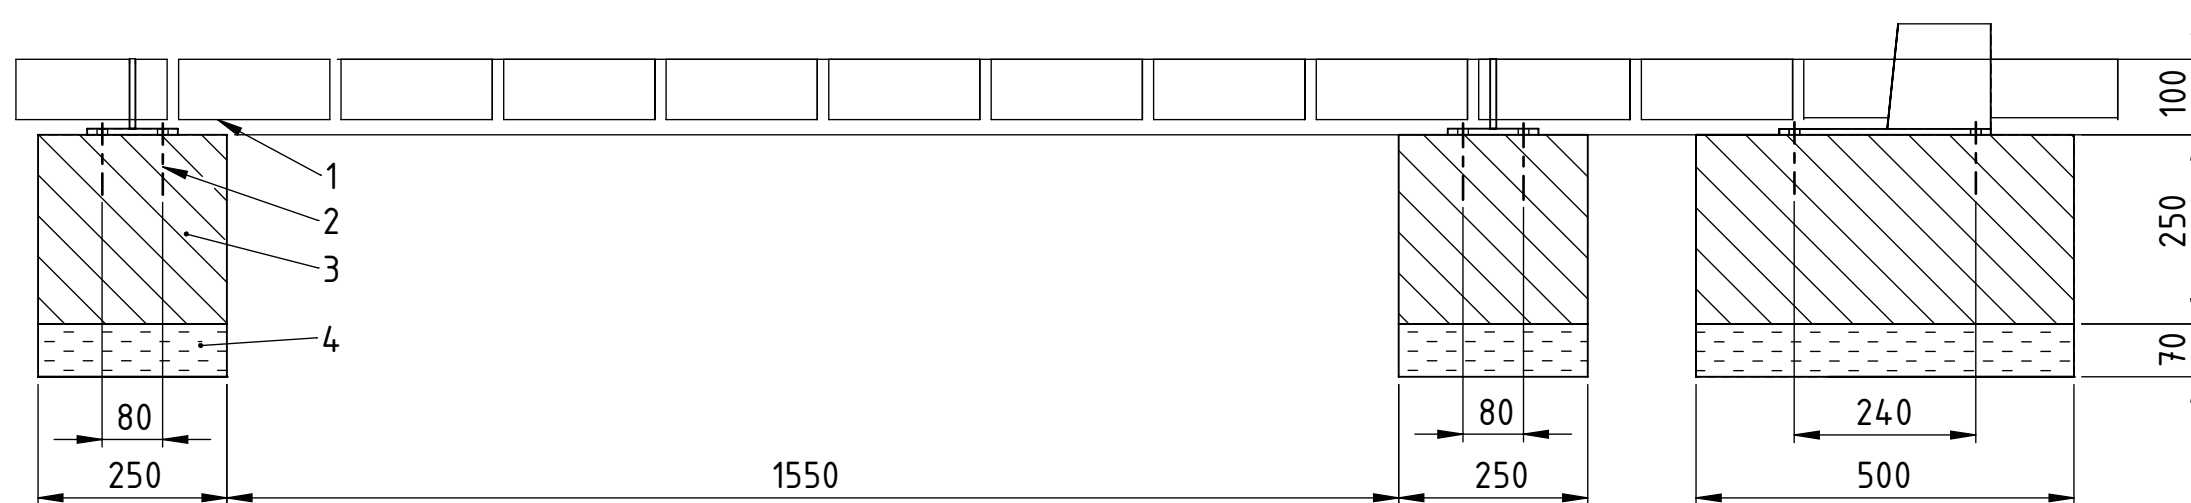
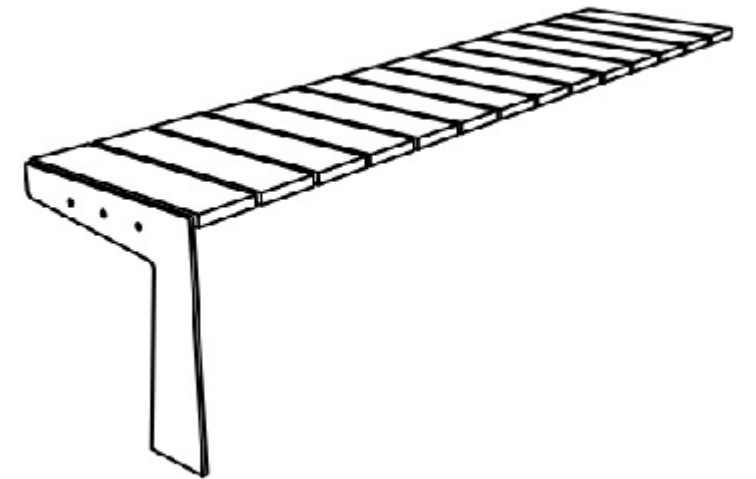


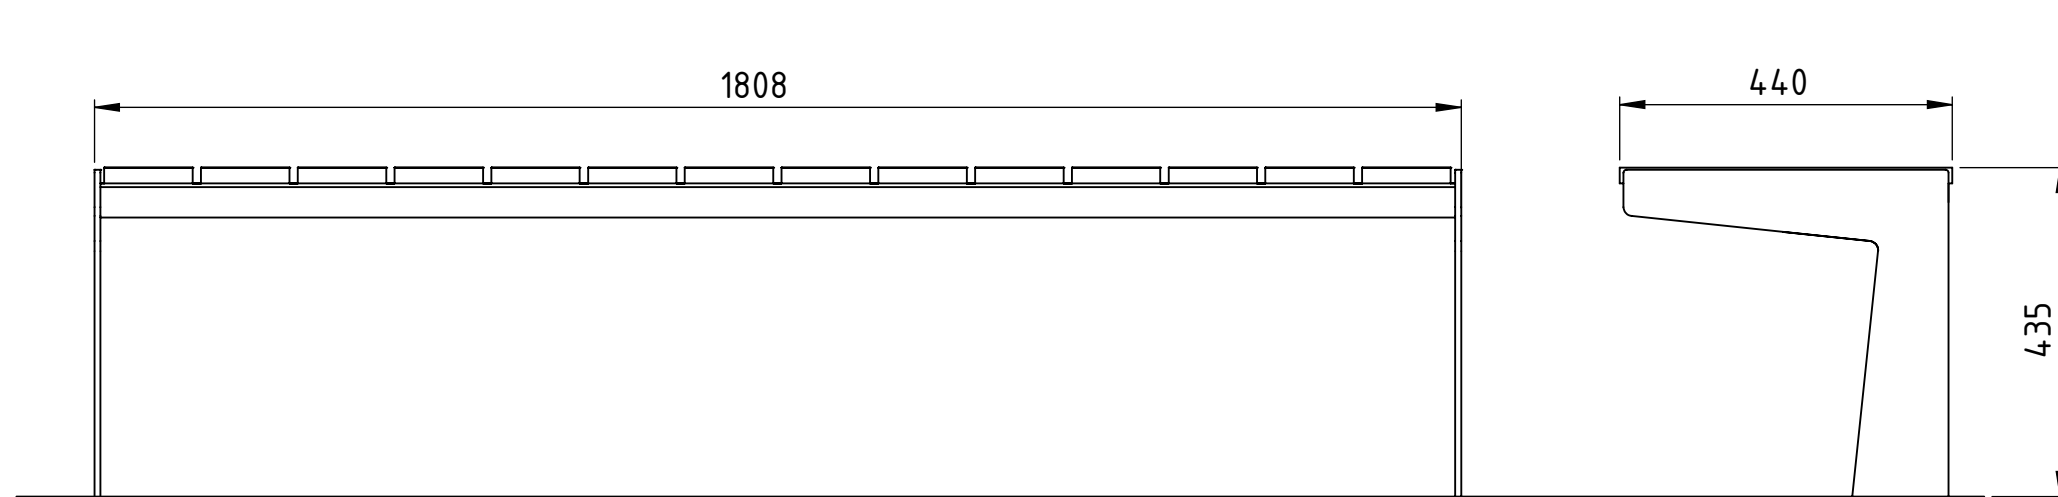

0,03 m3
beton C 12/15
concrete C 12/15

LEGEND:
1 Pavement
2 Chemical anchor M10, min.length 100mm
3 Concrete foundation
4 Compacted gravel base, min. depth 70mm