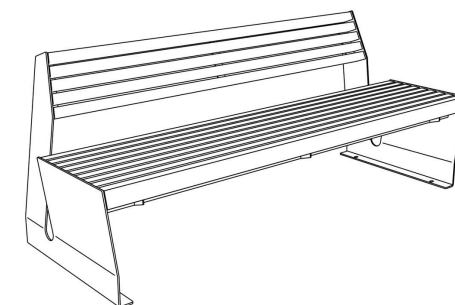
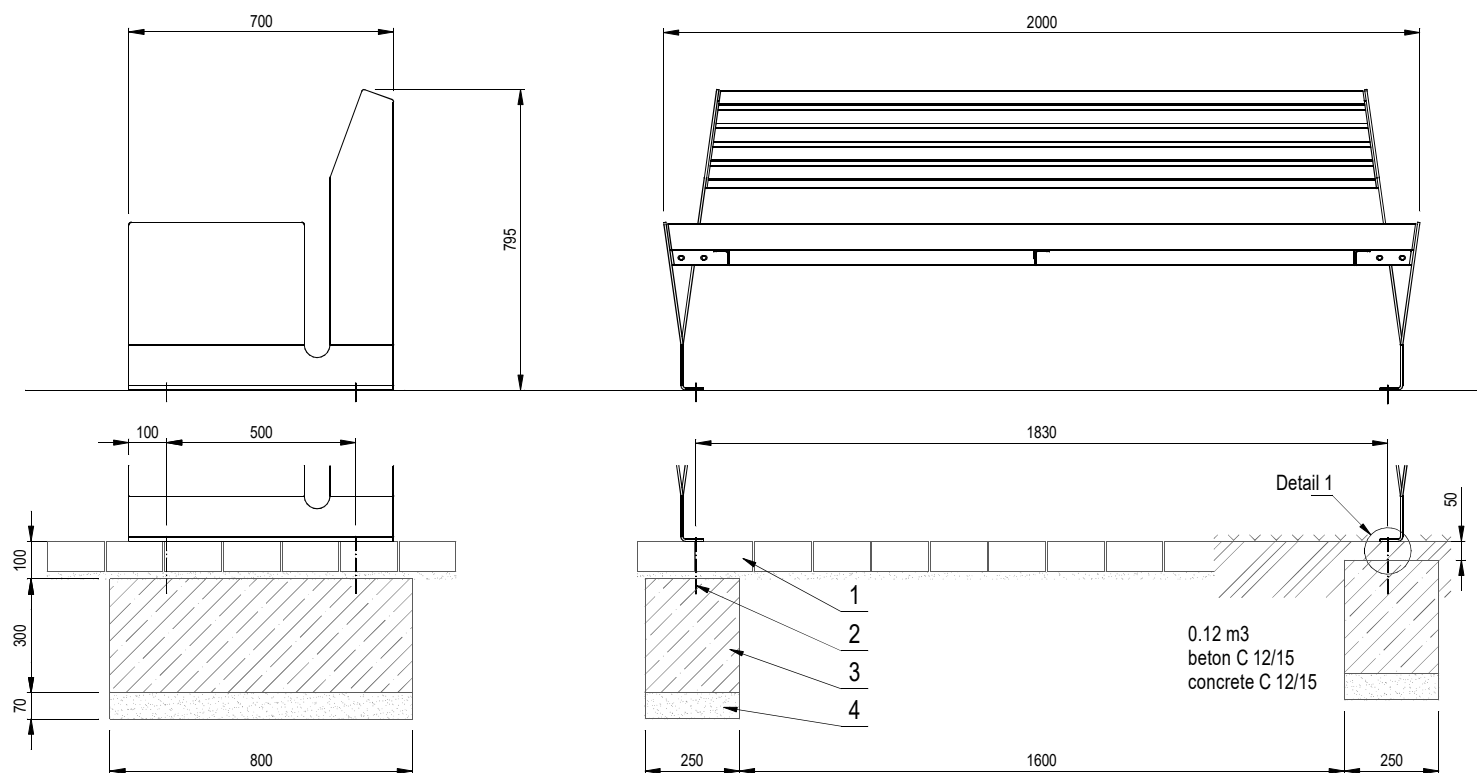


- LEGEND:
- 1 Pavement
 - 2 Chemical anchor M10, dl. min 100
 - 3 Concrete foundation
 - 4 Compacted gravel base, depth min. 70 mm
 - 5 Counter nuts (for soil foundation)

LVG120