
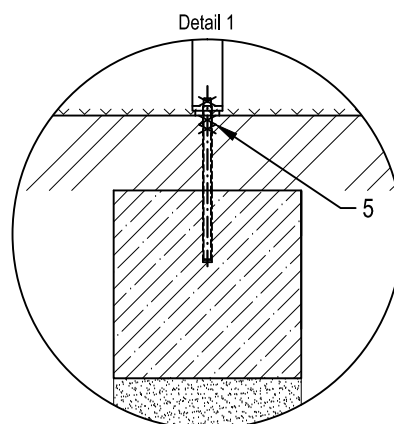
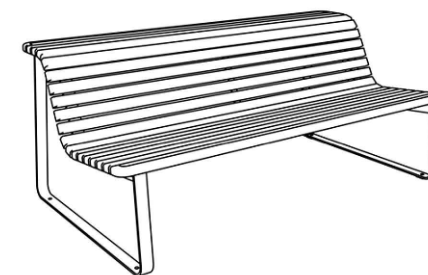


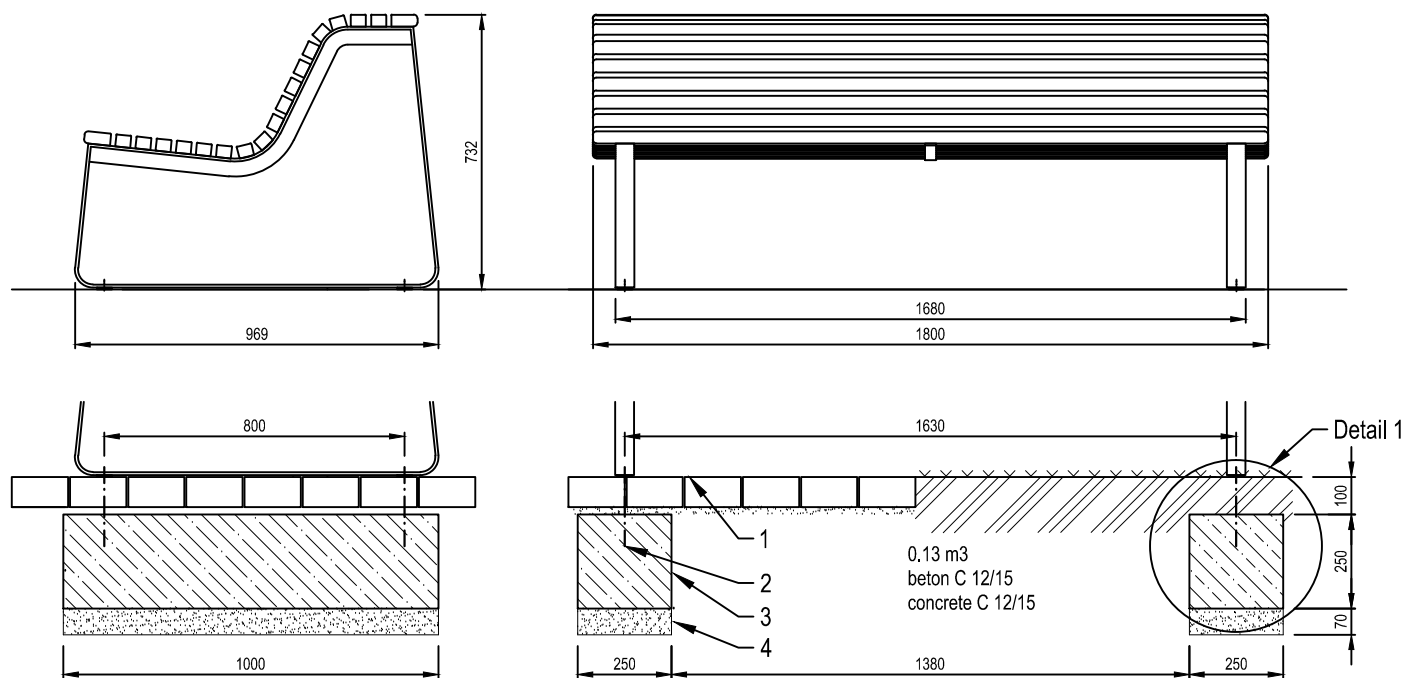

LEGEND:

- 1 Pavement
- 2 Chemical anchor M10, dl. min 200
- 3 Concrete foundation
- 4 Compacted gravel base, depth min. 70 mm
- 5 Counter nuts (for soil foundation)

LVL1 1800 mm

Všetchna práva vyhrazena. Chráněno průmyslovým vzorem.
All rights reserved. Protection of industrial design.

version: 2018/01

Dimensions of products, foundations and anchors are informative only. The exact dimensions you get with our offer.