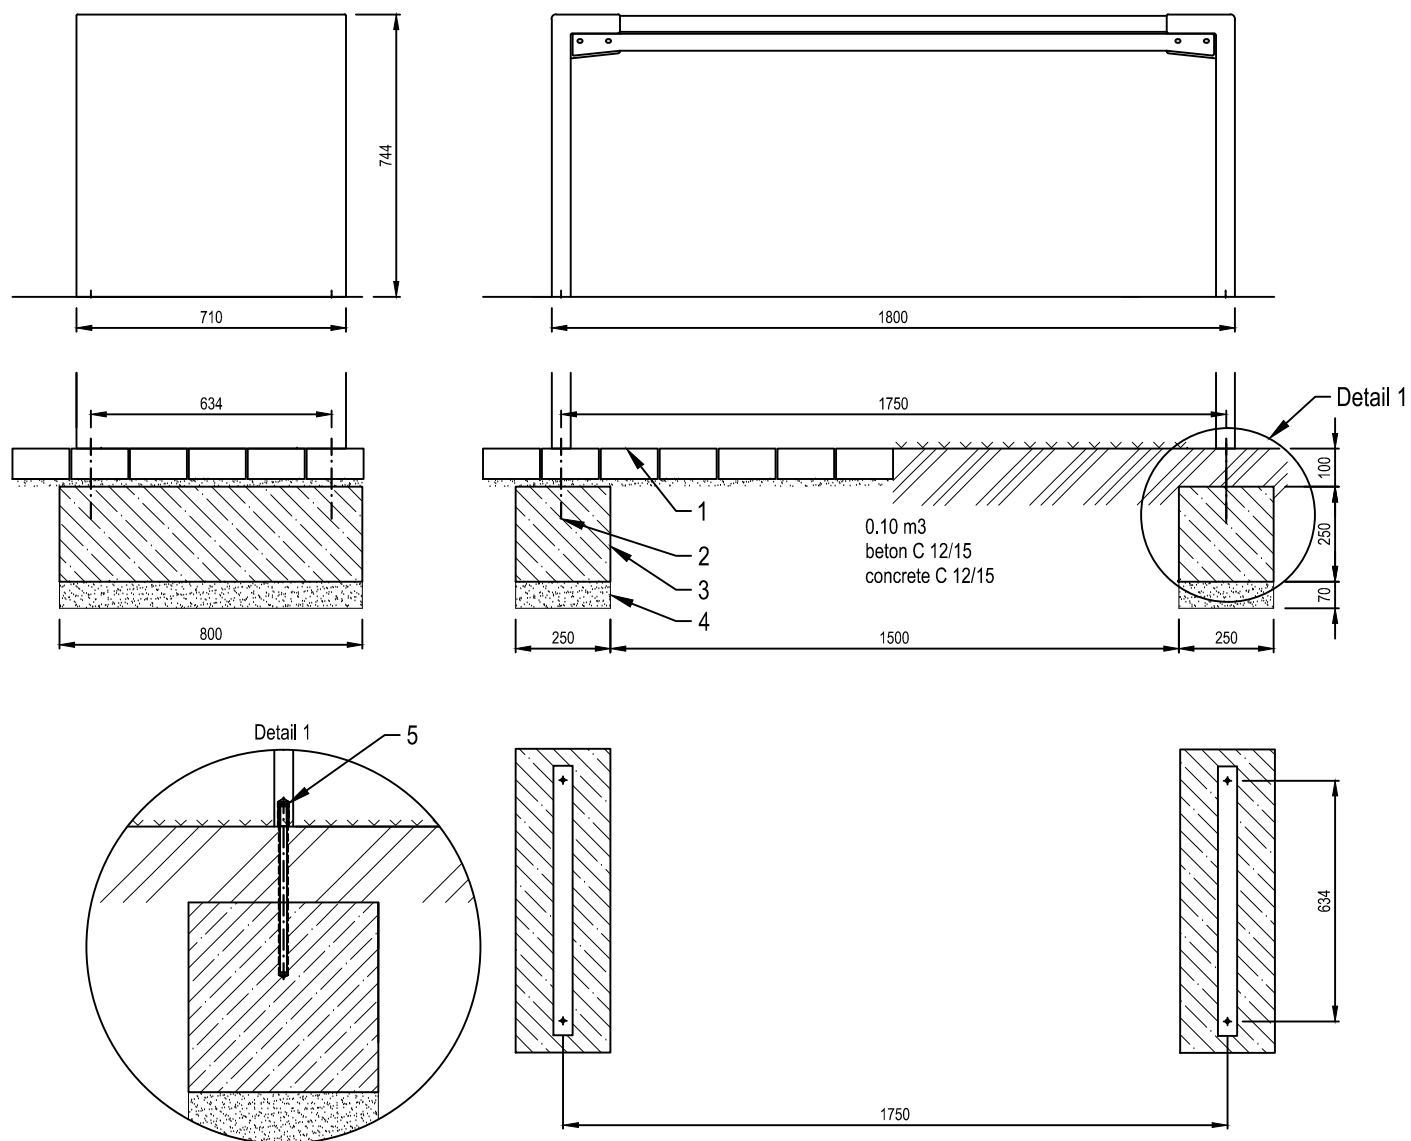


- LEGEND:
- 1 Pavement
 - 2 Chemical anchor M10, dl. min 200
 - 3 Concrete foundation
 - 4 Compacted gravel base, depth min. 70 mm
 - 5 Round long nut

SSB5/6 1800 mm

Všetchna práva vyhrazena. Chráněno průmyslovým vzorem.
All rights reserved. Protection of industrial design.

version: 2018/01