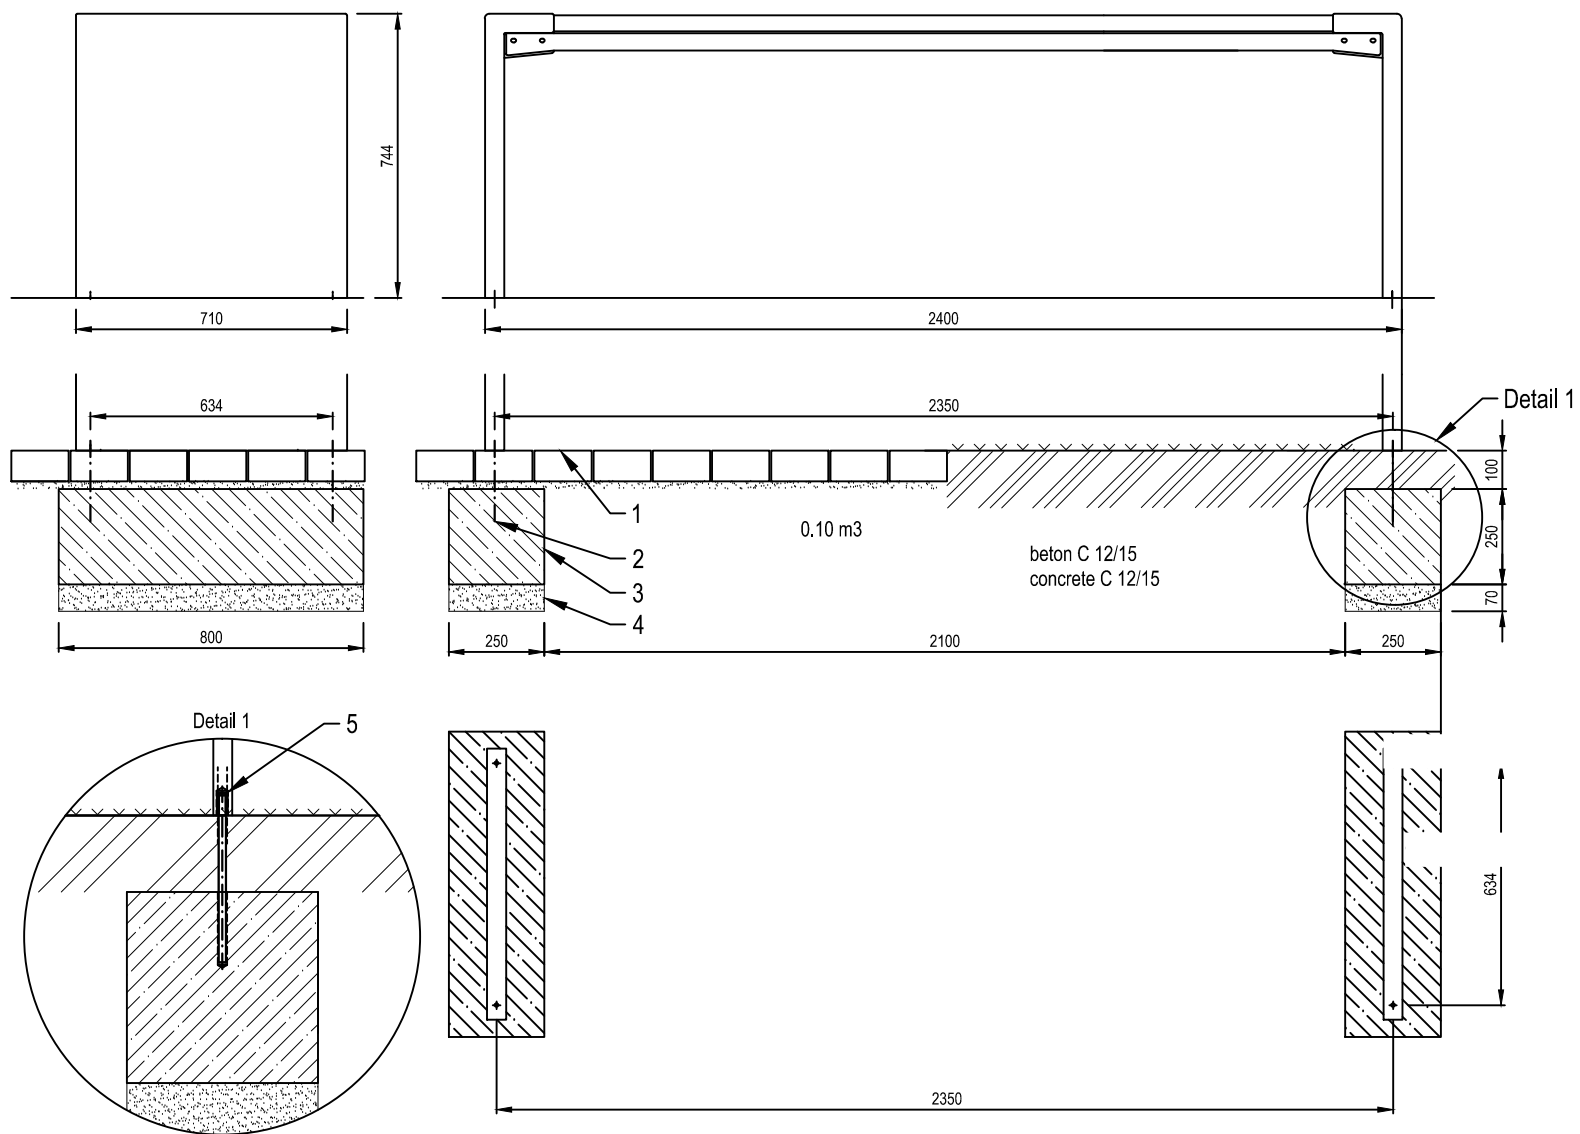


- LEGEND:**
- 1 Pavement
 - 2 Chemical anchor M10, dl. min 200
 - 3 Concrete foundation
 - 4 Compacted gravel base, depth min. 70 mm
 - 5 Round long nut

SSB7/8 2400 mm

Všetchna práva vyhrazena. Chráněno průmyslovým vzorem.
All rights reserved. Protection of industrial design.

version: 2019/03
streetpark.eu

Dimensions of products, foundations and anchors are informative only. The exact dimensions you get with our offer.